

I, JEREMY R. DAVIS, REGISTERED PROFESSIONAL LAND SURVEYOR, DO HEREBY CERTIFY THAT THE SURFACE LOCATION SHOWN HEREON WAS STAKED ON THE GROUND BY ME OR UNDER MY DIRECT SUPERVISION.

Jeremy R. Davis
JEREMY R. DAVIS, R.P.L.S. #6259
101 BRYANHURST ST.
HENDERSON, TEXAS 75654
PH (903) 693-1269

7/24/26
DATE



H.G. BECKER GAS UNIT
CALLED 704.00 AC.

J. PHILIP THOMPSON GAS UNIT
CALLED 648.71 AC.

SURFACE HOLE LOCATION (S.H.L.)

Y = 284390.5 (NAD27)
X = 2946117.6 (NAD27)
ELEV = 314.2' (NAVD88)
LAT. = 32° 24' 38.09" (NAD83)
LONG. = 94° 26' 02.63" (NAD83)
1896' FROM SOUTH UNIT LINE
717' FROM WEST UNIT LINE
1896' FROM SOUTH SURVEY LINE
1640' FROM WEST SURVEY LINE

POINT OF PENETRATION (P.O.P.)

Y = 286683.6 (NAD27)
X = 2947723.3 (NAD27)
LAT. = 32° 25' 00.30" (NAD83)
LONG. = 94° 25' 43.12" (NAD83)
100' FROM NORTH UNIT LINE
2758' FROM WEST UNIT LINE

FIRST TAKE POINT (F.T.P.)


Y = 286454.6 (NAD27)
X = 2947772.9 (NAD27)
LAT. = 32° 24' 58.02" (NAD83)
LONG. = 94° 25' 42.62" (NAD83)
330' FROM NORTH UNIT LINE
716' FROM EAST UNIT LINE

LAST TAKE POINT (L.T.P.)

Y = 274222.2 (NAD27)
X = 2950419.9 (NAD27)
LAT. = 32° 22' 56.26" (NAD83)
LONG. = 94° 25' 15.94" (NAD83)
243' FROM SW UNIT LINE
624' FROM SE UNIT LINE

TERMINUS POINT (T.P.)

Y = 274014.7 (NAD27)
X = 2950464.8 (NAD27)
LAT. = 32° 22' 54.20" (NAD83)
LONG. = 94° 25' 15.49" (NAD83)
100' FROM SW UNIT LINE
469' FROM SE UNIT LINE
100' FROM SW SURVEY LINE
469' FROM SE SURVEY LINE

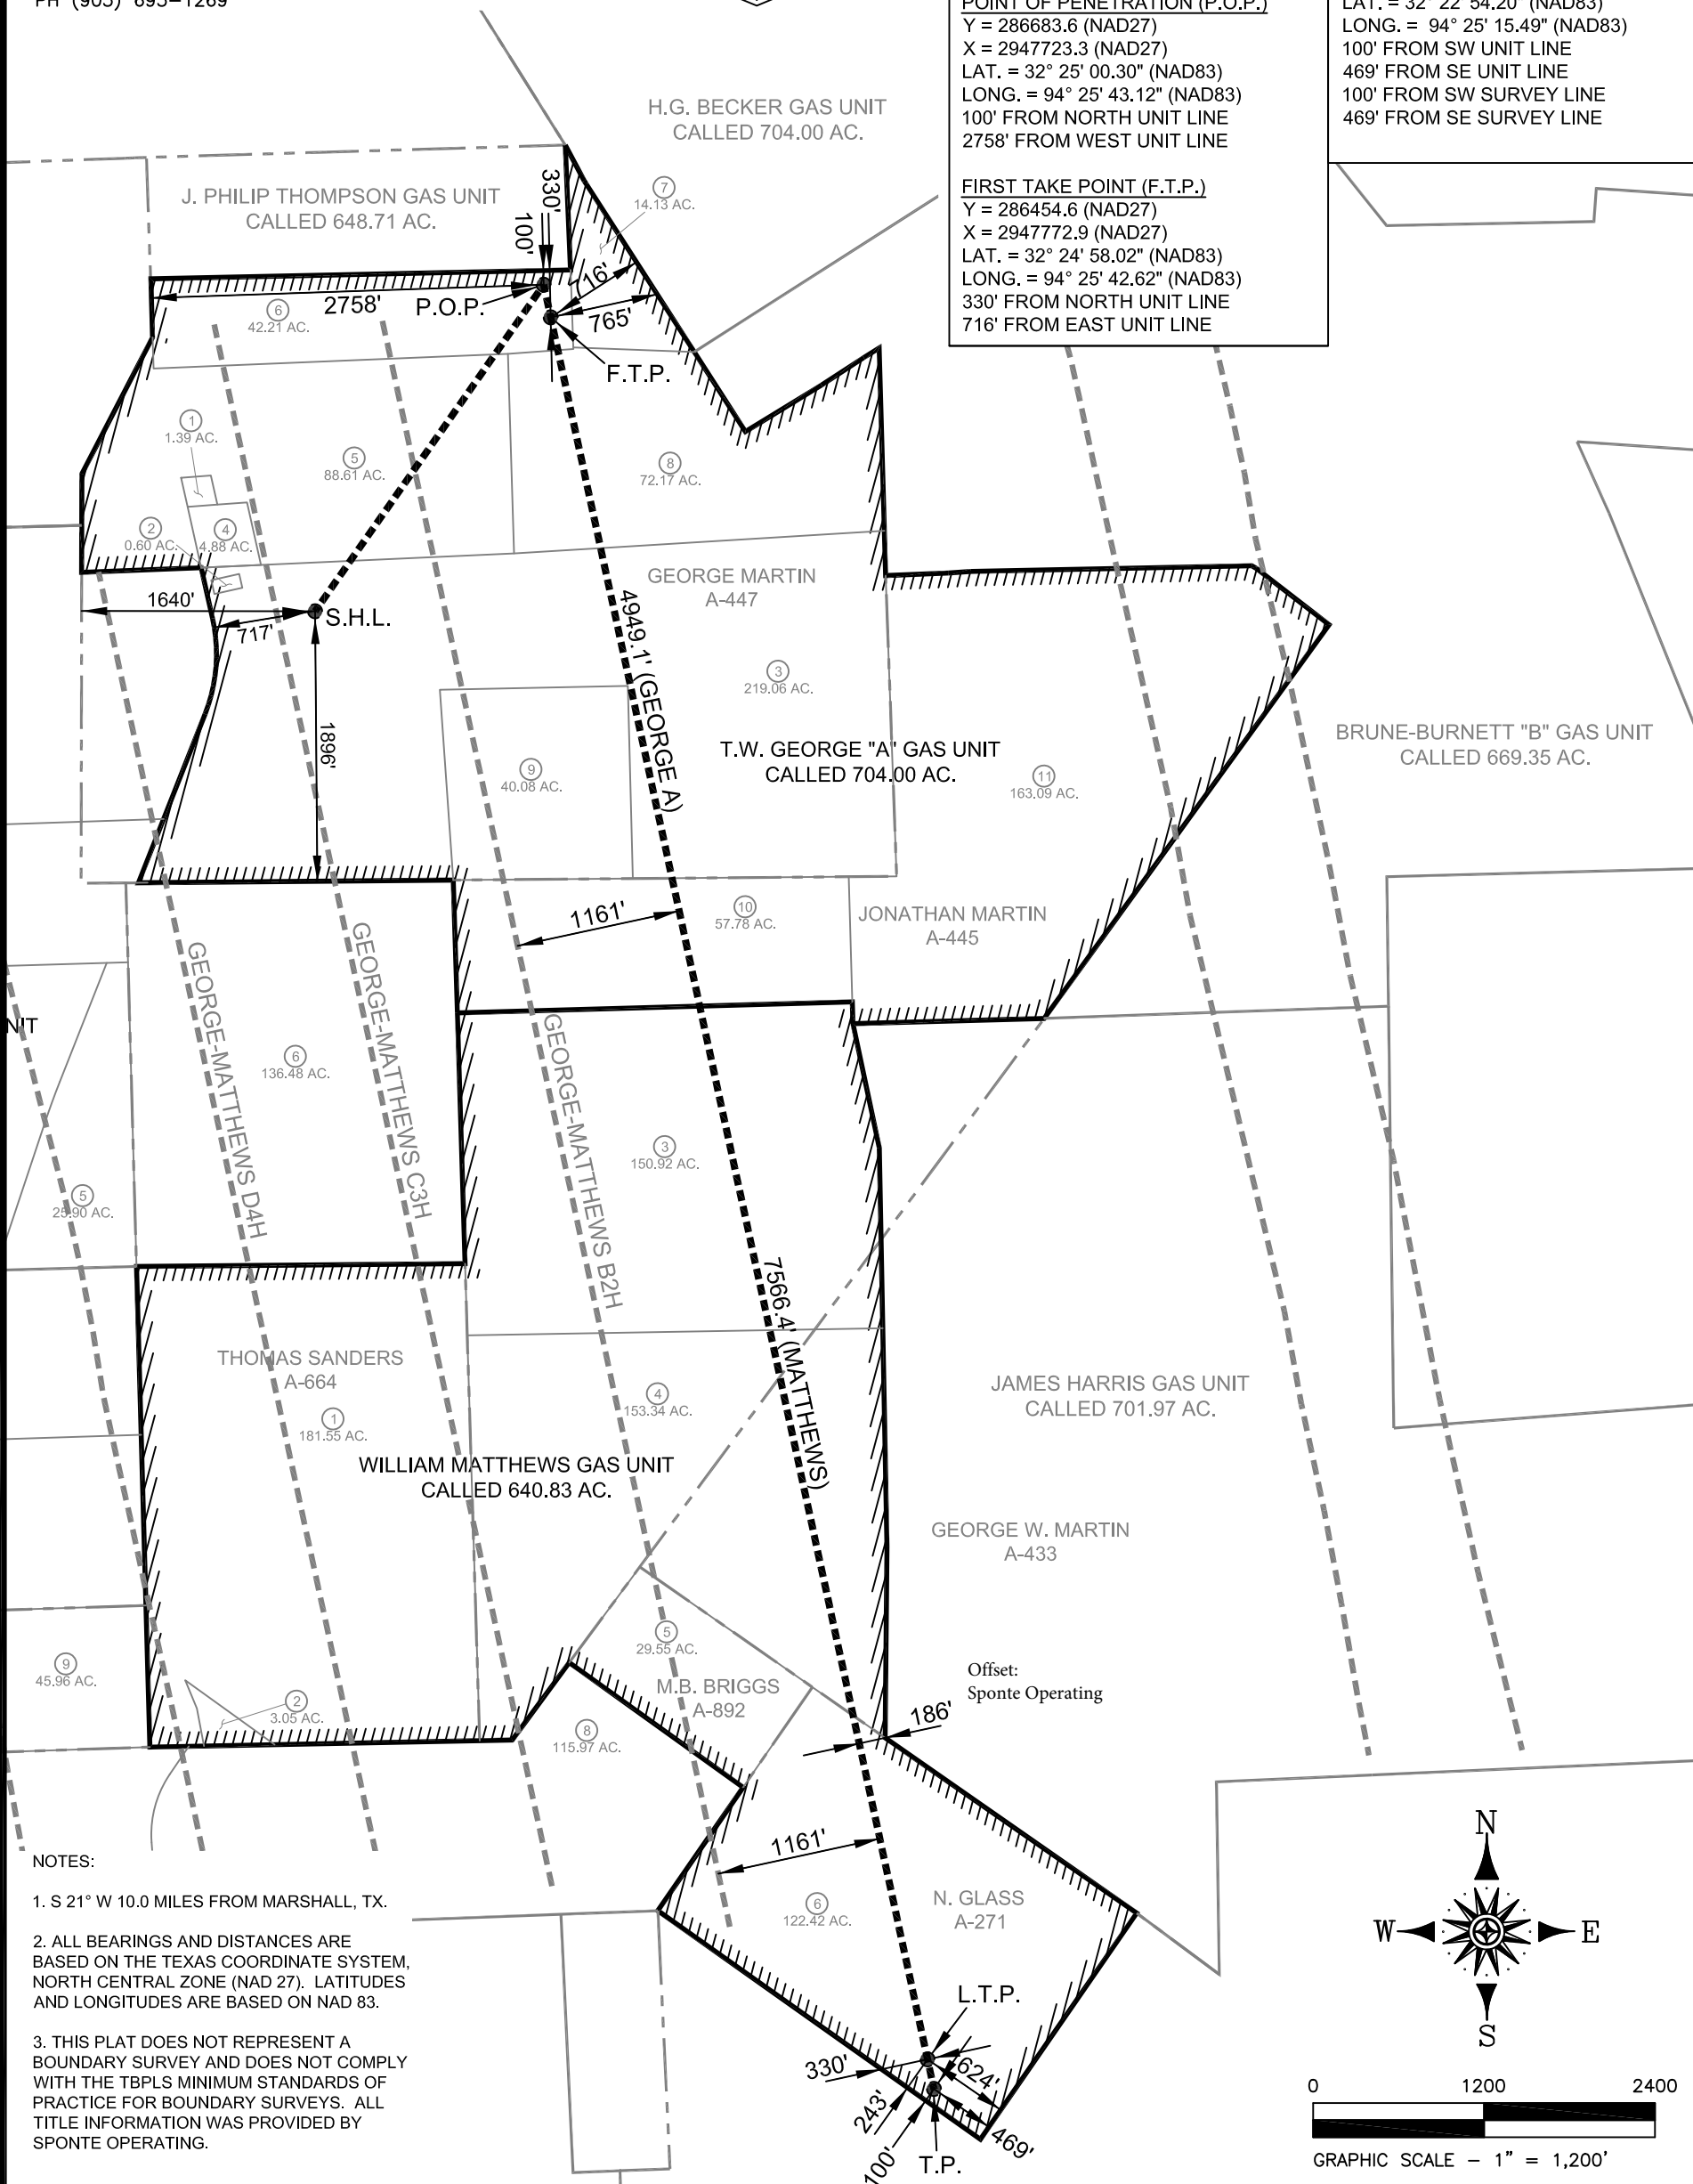

NOTES:

1. S 21° W 10.0 MILES FROM MARSHALL, TX.
2. ALL BEARINGS AND DISTANCES ARE BASED ON THE TEXAS COORDINATE SYSTEM, NORTH CENTRAL ZONE (NAD 27). LATITUDES AND LONGITUDES ARE BASED ON NAD 83.
3. THIS PLAT DOES NOT REPRESENT A BOUNDARY SURVEY AND DOES NOT COMPLY WITH THE TBPLS MINIMUM STANDARDS OF PRACTICE FOR BOUNDARY SURVEYS. ALL TITLE INFORMATION WAS PROVIDED BY SPONTE OPERATING.

DRILL PATH DISTANCES
SHL - POP = 2,799.4 FT.
POP - FTP = 234.3 FT.
FTP - LTP = 12,515.5 FT.
LTP - TP = 212.4 FT.

SPONTE OPERATING, INC.
GEORGE-MATTHEWS A1H
HARRISON COUNTY, TEXAS

RWD Engineering, Inc.
Civil Engineering/Land Surveying
101 Bryanhurst St.
Henderson, TX 75654
PH: 903.693.1269
Firm Reg. # - 10018000 (TBPLS)
Firm Reg. # - 8732 (TBPE)