


All Bearings, Distances, and Coordinates shown hereon are based on the Texas State Plane Coordinate System, N.A.D. 83 Datum (Central Zone.) Bearings are grid, convergence is at the Surface Location.

The information contained on this plat is intended for the sole use of EMPIRE TEXAS OPERATING LLC

This plat represents a survey which meets the requirements for filing a unit plat with the Texas Railroad Commission and is solely intended for that purpose.


Acreage's shown hereon were furnished by EMPIRE TEXAS OPERATING LLC and are deed called or scaled from deed.

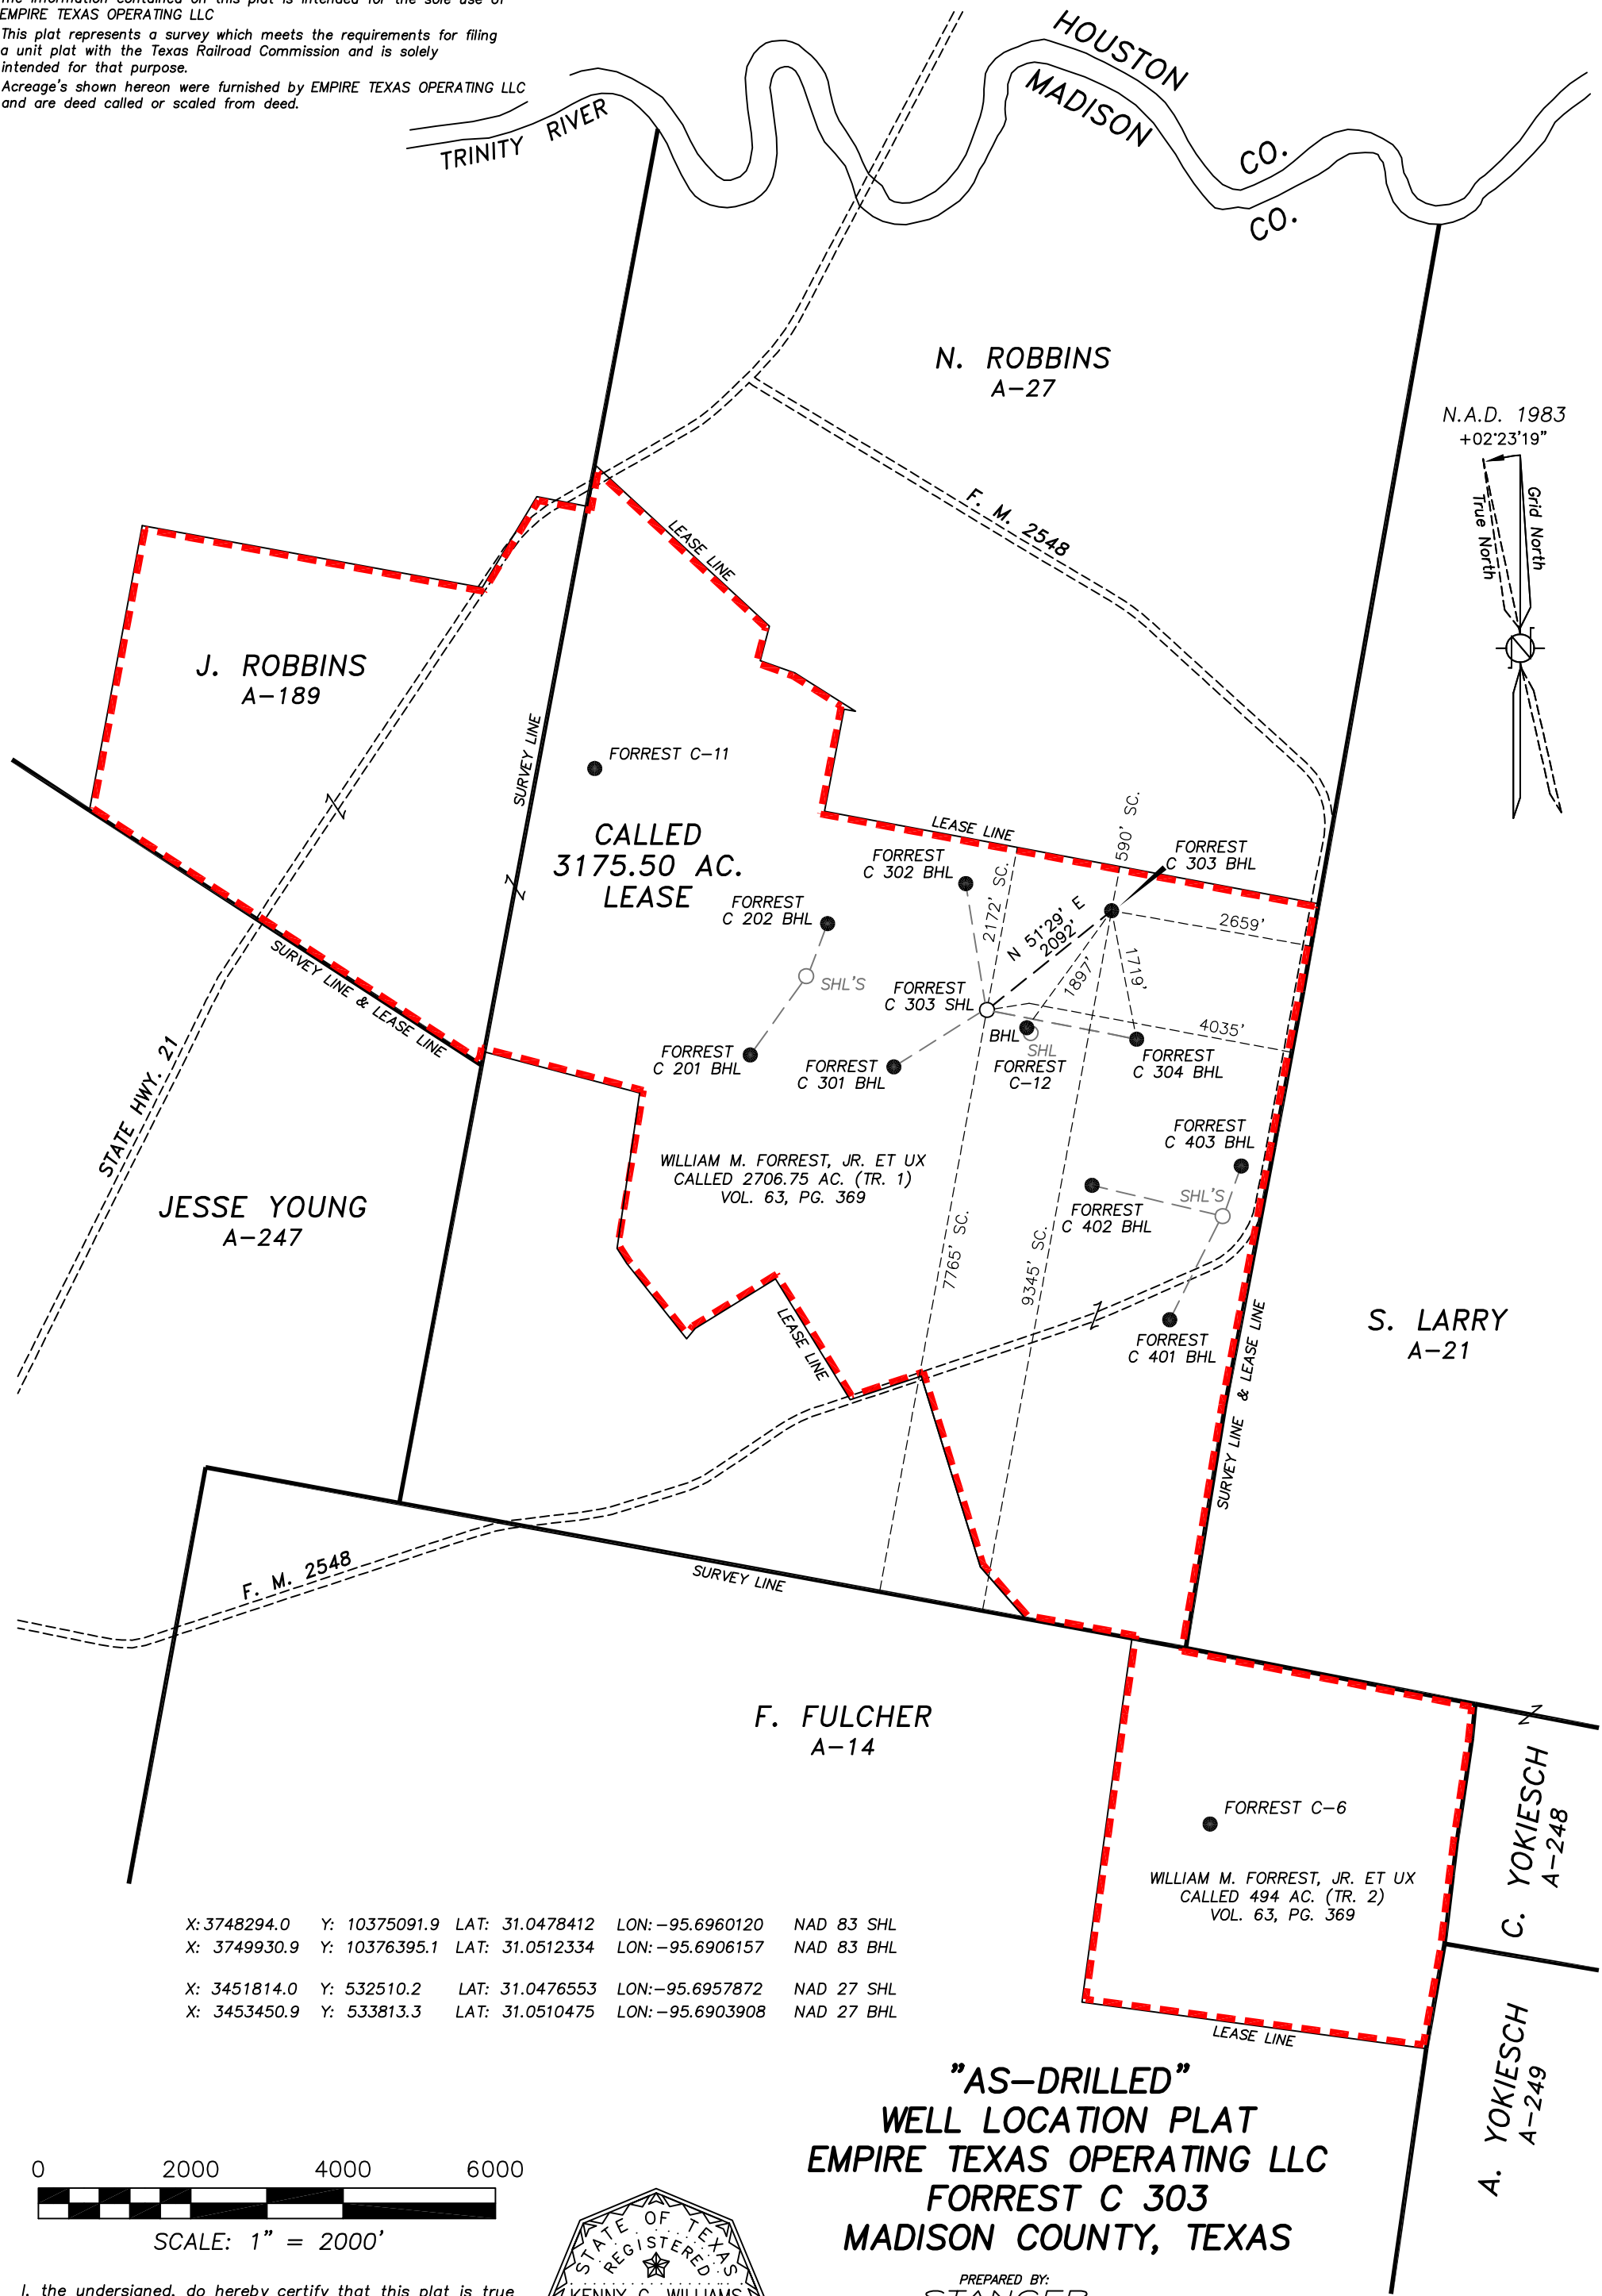

X: 3748294.0	Y: 10375091.9	LAT: 31.0478412	LON: -95.6960120	NAD 83 SHL
X: 3749930.9	Y: 10376395.1	LAT: 31.0512334	LON: -95.6906157	NAD 83 BHL
X: 3451814.0	Y: 532510.2	LAT: 31.0476553	LON: -95.6957872	NAD 27 SHL
X: 3453450.9	Y: 533813.3	LAT: 31.0510475	LON: -95.6903908	NAD 27 BHL

0 2000 4000 6000

SCALE: 1" = 2000'

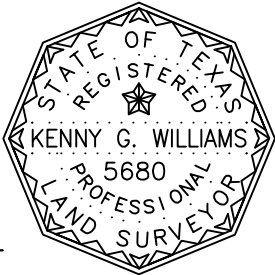

I, the undersigned, do hereby certify that this plat is true and correct to the best of my knowledge and belief.

BY: *Kenny Williams* DATE: 8/3/26

"AS-DRILLED"
WELL LOCATION PLAT
EMPIRE TEXAS OPERATING LLC
FORREST C 303
MADISON COUNTY, TEXAS

PREPARED BY:
STANGER
SURVEYING TYLER LLC
1595 EAST GRANDE BLVD.
TYLER, TEXAS 75703
(903) 534-0174

"SAND RIDGE" Quadrangle
Sited 14.5 Miles ENE of Madisonville, TX.
SHL Natural Ground Elev. = 154'
T260209-FORREST C #303 AS-DRILLED