


**PLAT SHOWING THE LOCATION OF
CHISOS, LTD.
PERRY WELL No. 1
IN THE ABRAHAM DARST SURVEY, ABSTRACT No. 61
BRAZORIA COUNTY, TEXAS**

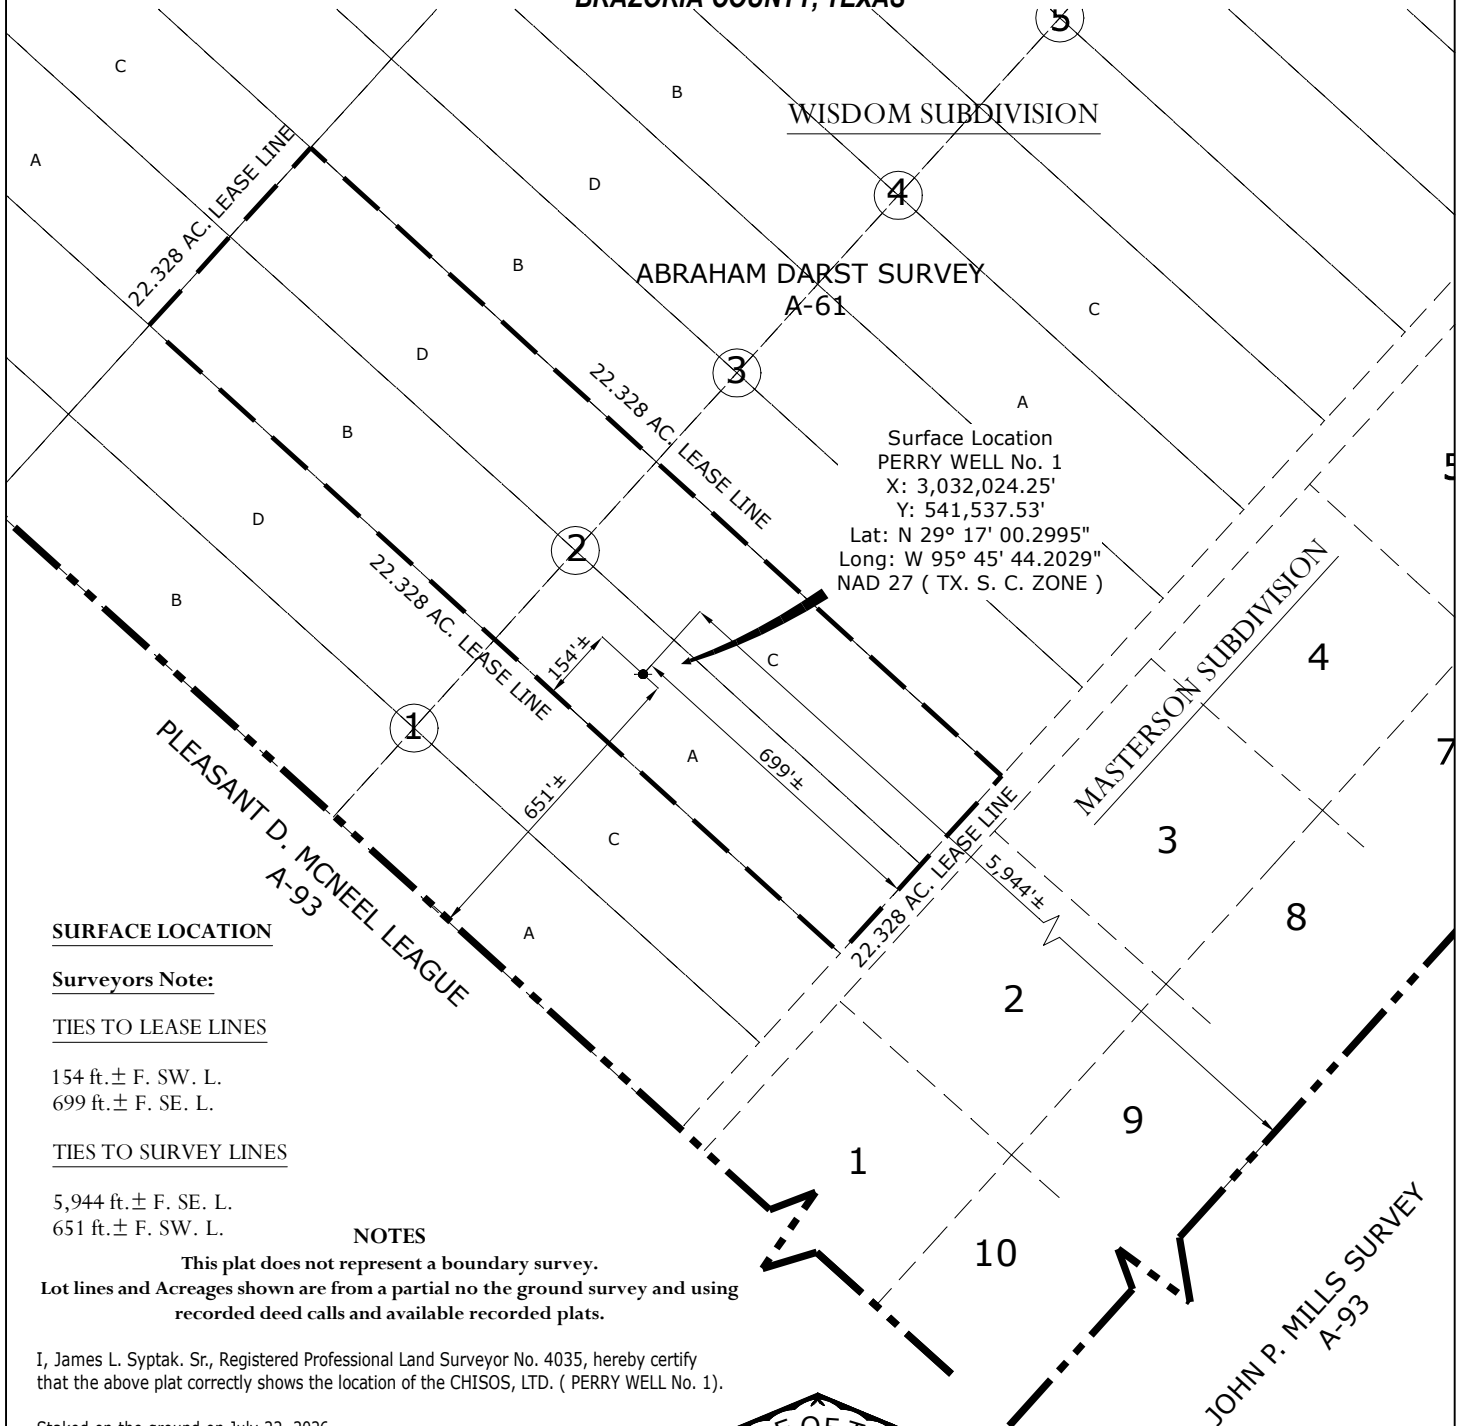

SURFACE LOCATION

Surveyors Note:

TIES TO LEASE LINES

154 ft. ± F. SW. L.
699 ft. ± F. SE. L.

TIES TO SURVEY LINES

5,944 ft. ± F. SE. L.
651 ft. ± F. SW. L.

NOTES

This plat does not represent a boundary survey.
Lot lines and Acreages shown are from a partial no the ground survey and using
recorded deed calls and available recorded plats.

I, James L. Syptak, Sr., Registered Professional Land Surveyor No. 4035, hereby certify
that the above plat correctly shows the location of the CHISOS, LTD. (PERRY WELL No. 1).

Staked on the ground on July 22, 2026.

Date of Plat or Map: July 24, 2026.


James L. Syptak, Sr.
(James L. Syptak, SR.)
Registered Professional Land Surveyor No. 4035

Note: Distance from the nearest town, bears S. 70 deg. W., 1.7 miles from the
U. S. Post Office in Damon, Texas more or less.

0 400 800 1200



Scale: 1" = 400'

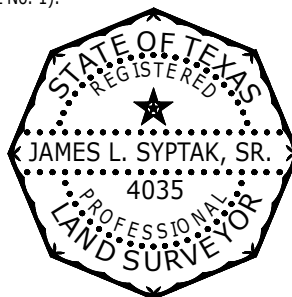

G&G Survey and Consulting, Inc.

Firm No. 10194937

9226 Needville Fairchilds Road

979-793-3428

email: gps01@comcast.net

Project No. 2026-123