



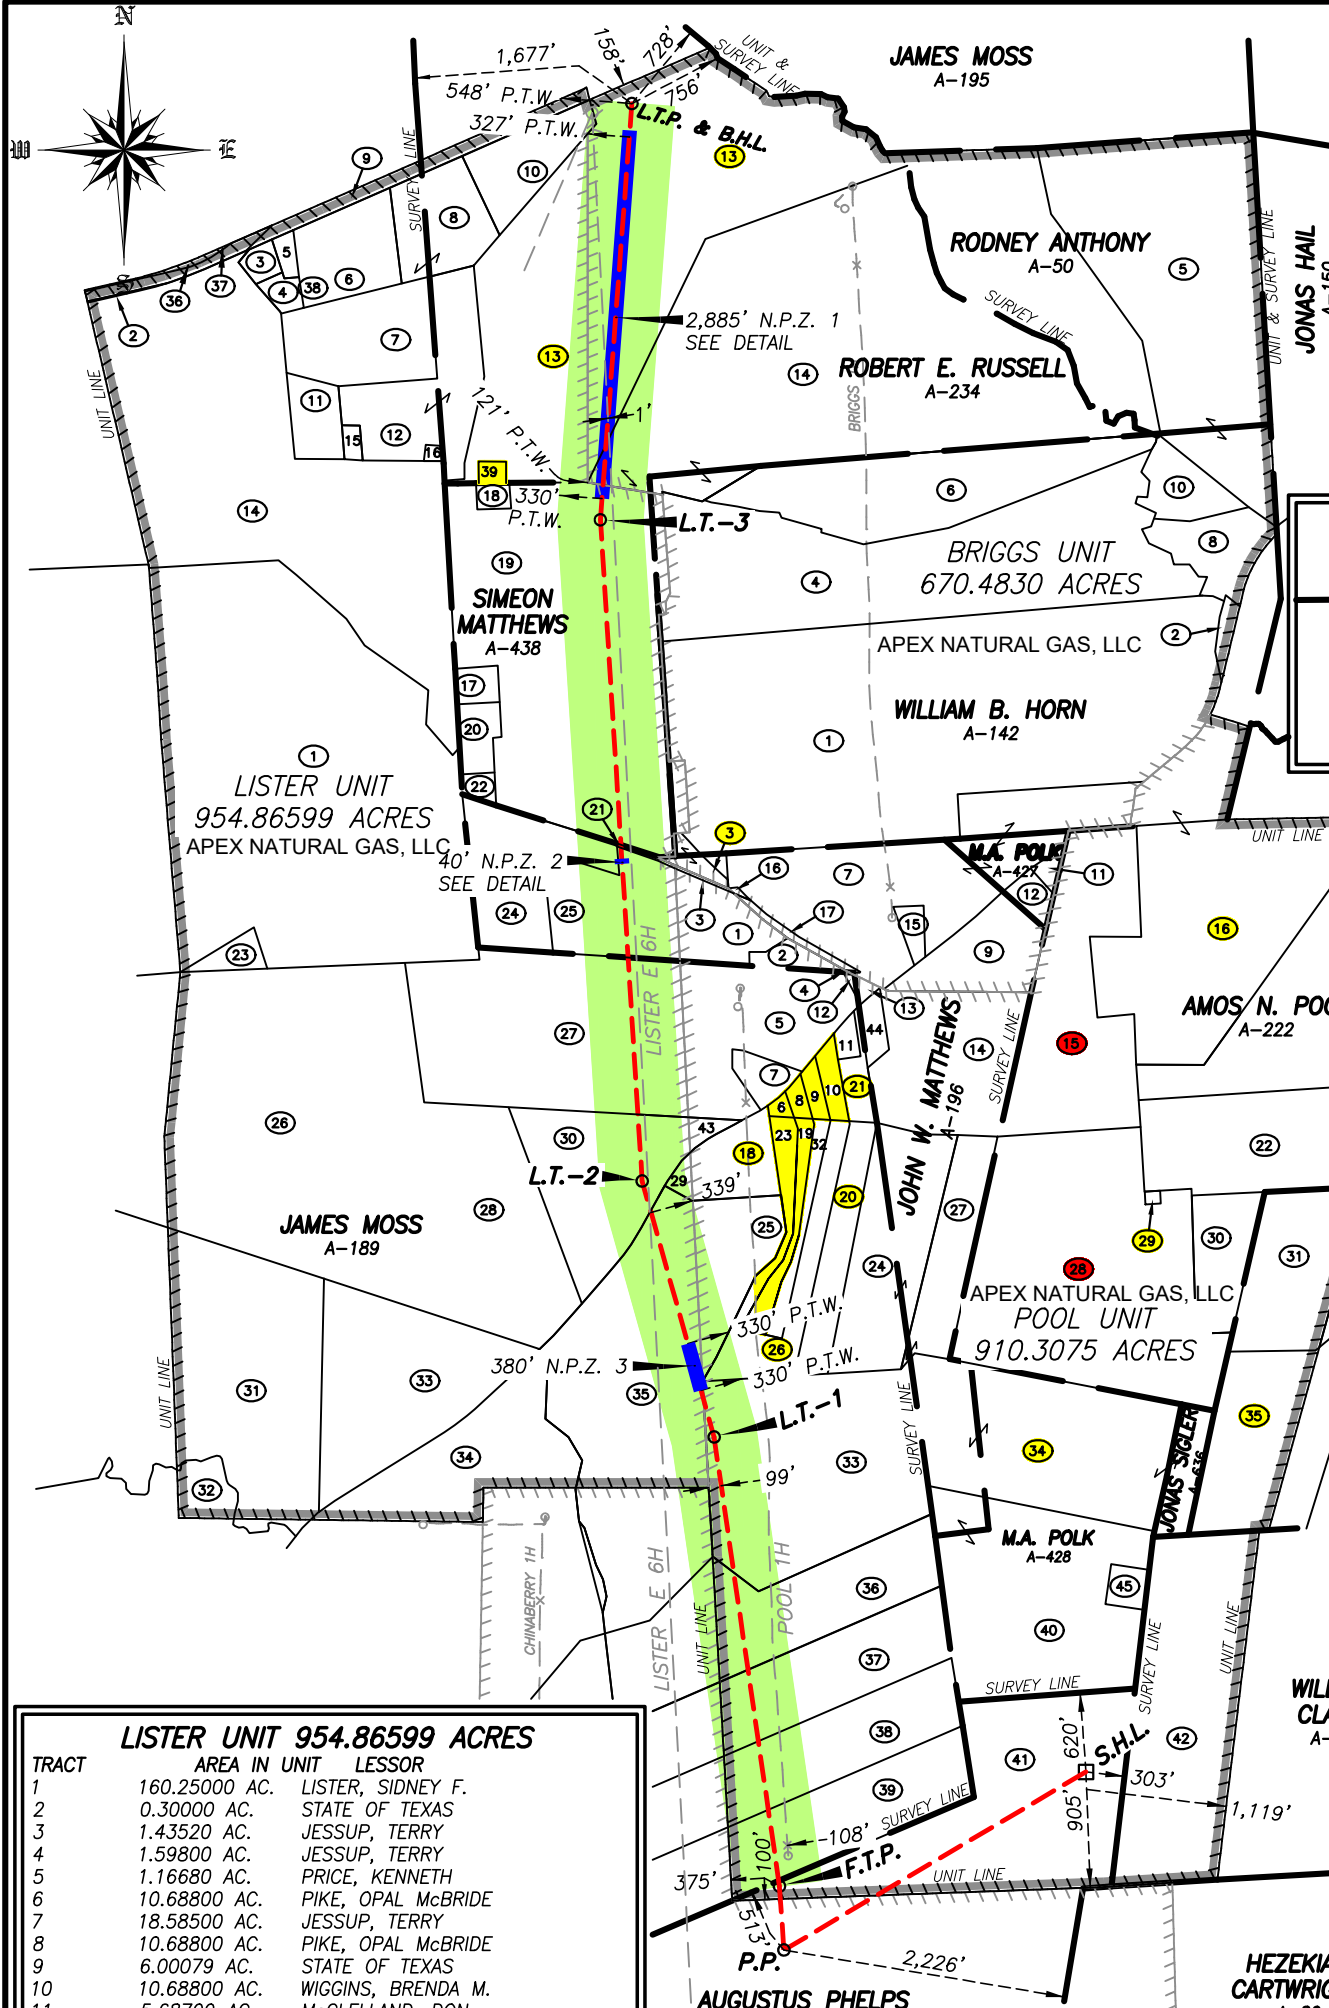

BRIGGS UNIT 670.4830 ACRES		
TRACT	AREA IN UNIT	LESSOR
1	152.0600 AC.	BRIGGS, KAREN L. TORKELSON, ET AL
2	0.9200 AC.	BRIGGS, KAREN L. TORKELSON, ET AL
3	1.9100 AC.	BRIGGS, KAREN L. TORKELSON, ET AL
4	80.3600 AC.	BRIGGS, KAREN L. TORKELSON, ET AL
5	65.6600 AC.	OGLESBEE, BETTY WOOD, ET AL
6	33.6400 AC.	BRIGGS, KAREN L. TORKELSON, ET AL
7	49.2500 AC.	PARTIN, WILLIAM MICHAEL, ET AL
8	9.6970 AC.	OGLESBEE, BETTY WOOD, ET AL
9	12.5000 AC.	PARTIN, WILLIAM MICHAEL
10	6.4000 AC.	PARTIN, WILLIAM MICHAEL, ET AL
11	1.0000 AC.	PARTIN, ROBERT VERNON
12	2.1700 AC.	CARROLL, MOLLIE SUE PARTIN
13	75.1560 AC.	GERALD W. THOMAS, ET AL
14	176.9000 AC.	DICKERSON, MARION FAY, ET AL
15	1.5000 AC.	PERRY, WILLIAM R., ET AL
16	0.1200 AC.	PERRY, WILLIAM R., ET AL
17	1.2400 AC.	PERRY, WILLIAM R., ET AL

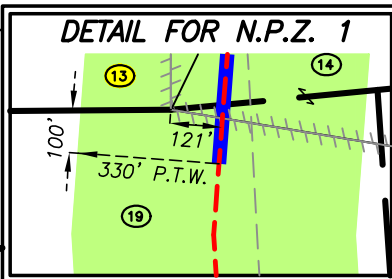


PROPOSED LATERAL TIES

S.H.L.
620' TO N LINE A-223
303' TO E LINE A-223
905' TO S LINE UNIT
1,119' TO E LINE UNIT

P.P.
513' TO NW LINE A-223
2,226' TO E LINE A-223

F.T.P.
100' TO S LINE UNIT
375' TO W LINE UNIT

L.T.P./B.H.L.
158' TO NW LINE UNIT
756' TO NE LINE UNIT
728' TO NE LINE A-234
1,677' TO W LINE A-234

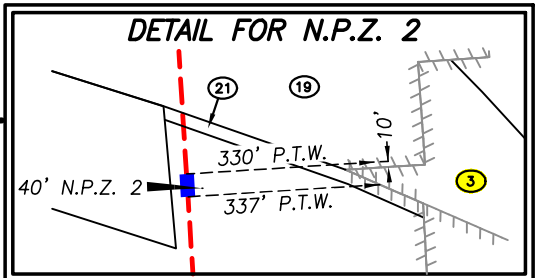

POOL UNIT 910.3075 ACRES		
TRACT	AREA IN UNIT	LESSOR
1	8.7800 AC.	MASON MARTINDALE GROUP, L.P.
2	2.8780 AC.	MASON MARTINDALE GROUP, L.P.
3	0.2610 AC.	MASON MARTINDALE GROUP, L.P.
4	0.1330 AC.	MASON MARTINDALE GROUP, L.P.
5	17.7000 AC.	LISTER, LYNN M.
6	0.2402 AC.	DAVIS, LUNCH, HEIRS OF
7	2.3000 AC.	ST. LUKE'S CEMETERY
8	0.8977 AC.	SEXTON, LILLIE MAE MATHEWS
9	1.2118 AC.	MATHEWS, JAKE
10	1.8541 AC.	MATHEWS, CLYDE, HEIRS OF
11	1.0000 AC.	ST. LUKE MISSIONARY BAPTIST
12	0.1830 AC.	WISE, RAYMOND
13	0.5450 AC.	LISTER, JR., L.W.
14	27.4900 AC.	MARTINDALE LAND & CATTLE CO.
15	37.9970 AC.	EXXON MOBIL CORPORATION
16	65.8540 AC.	MATHEWS, JANET
17	57.5190 AC.	MATHEWS, JANET
18	7.4100 AC.	BURNETT, CHERRY MATHEWS
19	4.3620 AC.	MATHEWS, ROBERT BRAD
20	10.5641 AC.	MATHEWS, JOHN RICHARD
21	2.7059 AC.	HOLMAN, EVON, HEIRS OF
22	56.5000 AC.	BOWMAN, JOEL
23	4.8598 AC.	MATHEWS, ROBERT BRAD
24	26.5400 AC.	MATHEWS, ROBERT BRAD
25	22.6614 AC.	MATHEWS, ROBERT BRAD
26	11.4159 AC.	BLACKSTOCK, ROSEMARY MATHEWS
27	13.2700 AC.	BURNETT, CHERRY MATHEWS
28	77.0000 AC.	EXXON MOBIL CORPORATION
29	1.5000 AC.	RAMSEY, OPAL OWENS
30	10.0000 AC.	BOWMAN, JOEL
31	19.5000 AC.	BOWMAN, JOEL
32	3.8882 AC.	MATHEWS, JAKE
33	51.5000 AC.	LANE, BOBBIE
34	47.1816 AC.	ROBERTS, KATHLEEN M.
35	20.7726 AC.	DeBOLT, PAULA J. WHITTON
36	27.3650 AC.	MATHEWS, ROBERT BRAD
37	28.6966 AC.	MITCHELL, PATSY HAGAN
38	30.1106 AC.	MORRIS, ROBERT GLENN
39	27.4152 AC.	MATHEWS, JACK BLANTON
40	47.2000 AC.	DeBOLT, PAULA J. WHITTON
41	74.0595 AC.	SHARP, SARAH C.
42	50.0000 AC.	OLIPHANT, WINNIE
43	1.9853 AC.	BLACKSTOCK, ROSEMARY MATHEWS
44	2.0000 AC.	SAN AUGUSTINE I.S.D.
45	3.0000 AC.	C. R. MITCHELL FAMILY LTD.

LISTER UNIT 954.86599 ACRES		
TRACT	AREA IN UNIT	LESSOR
1	160.25000 AC.	LISTER, SIDNEY F.
2	0.30000 AC.	STATE OF TEXAS
3	1.43520 AC.	JESSUP, TERRY
4	1.59800 AC.	JESSUP, TERRY
5	1.16680 AC.	PRICE, KENNETH
6	10.68800 AC.	PIKE, OPAL McBRIDE
7	18.58500 AC.	JESSUP, TERRY
8	10.68800 AC.	PIKE, OPAL McBRIDE
9	6.00079 AC.	STATE OF TEXAS
10	10.68800 AC.	WIGGINS, BRENDA M.
11	5.68700 AC.	McCLELLAND, DON
12	21.04120 AC.	FITZGERALD, DOUGLAS C.
13	41.66400 AC.	THOMAS FAMILY L.P.
14	111.73200 AC.	BLOUNT FAMILY PARTNERSHIP L.P.
15	0.86800 AC.	FITZGERALD, DOUGLAS C.
16	0.36500 AC.	PRICE, KENNETH
17	2.00000 AC.	OLD UNION S.C.C ASSOCIATION
18	1.16000 AC.	CARTWRIGHT, FORD SPARKS
19	91.20200 AC.	THE RICHEY TRUST
20	3.50000 AC.	T.A.C. UNITED METHODIST CHURCH
21	0.26100 AC.	MASON MARTINDALE GROUP, LP
22	1.50000 AC.	OLD UNION S.C.C ASSOCIATION
23	2.70000 AC.	BLACKSTOCK, ROSEMARY MATHEWS
24	18.33000 AC.	MARTINDALE LAND & CATTLE CO.
25	18.50000 AC.	MASON MARTINDALE GROUP, LP
26	90.60510 AC.	STETKA, LIBOR
27	54.25000 AC.	LISTER, PATRICK H.
28	66.72000 AC.	BLACKSTOCK, ROSEMARY MATHEWS
29	1.20000 AC.	BURNETT, CHERRY MATHEWS
30	20.64370 AC.	BLACKSTOCK, ROSEMARY MATHEWS
31	41.75960 AC.	BURNETT, CHERRY MATHEWS
32	4.52550 AC.	BLACKSTOCK, ROSEMARY MATHEWS
33	39.24100 AC.	BURNETT, CHERRY MATHEWS
34	33.93450 AC.	MATHEWS, JOHN RICHARD
35	55.05860 AC.	MATHEWS, ROBERT BRAD
36	0.25000 AC.	STATE OF TEXAS
37	0.02900 AC.	STATE OF TEXAS
38	4.00900 AC.	MILDRED McBRIDE TANNERY
39	0.73000 AC.	SHARP, SARAH C.

SURFACE LOCATION (S.H.L.)			ELEV. 345'
SPC TXC NAD 27	N:716,650.89	E:3,918,080.98	
GEOGRAPHIC NAD 27	LAT:31°29'28.25"	LON:94°10'35.47"	
PENETRATION POINT (P.P.)			
SPC TXC NAD 27	N:715,258.71	E:3,915,720.92	
GEOGRAPHIC NAD 27	LAT:31°29'15.79"	LON:94°11'03.58"	
FIRST TAKE POINT (F.T.P.)			
SPC TXC NAD 27	N:715,757.49	E:3,915,686.04	
GEOGRAPHIC NAD 27	LAT:31°29'20.73"	LON:94°11'03.66"	
LATERAL TURN 1 (L.T.-1)			
SPC TXC NAD 27	N:719,266.65	E:3,915,175.34	
GEOGRAPHIC NAD 27	LAT:31°29'55.69"	LON:94°11'07.31"	
LATERAL TURN 2 (L.T.-2)			
SPC TXC NAD 27	N:721,266.65	E:3,914,613.45	
GEOGRAPHIC NAD 27	LAT:31°30'15.76"	LON:94°11'12.52"	
LATERAL TURN 3 (L.T.-3)			
SPC TXC NAD 27	N:726,432.99	E:3,914,286.83	
GEOGRAPHIC NAD 27	LAT:31°31'07.00"	LON:94°11'12.99"	
LAST TAKE POINT/BOTTOM HOLE LOCATION (L.T.P./B.H.L.)			
SPC TXC NAD 27	N:729,684.68	E:3,914,532.59	
GEOGRAPHIC NAD 27	LAT:31°31'39.00"	LON:94°11'08.08"	

UNIT	AREA	PRODUCTIVE LATERAL
BRIGGS	670.4830 AC.	2988.27' (NO N.P.Z.)
LISTER	954.86599 AC.	7,222.84' (NO N.P.Z.)
POOL	910.3075 AC.	3,850.13' (NO N.P.Z.)
TOTAL	2,535.65649 AC.	14,061.24' (NO N.P.Z.)

PREPARED BY:
STANGER
SURVEYING TYLER LLC
1595 E. GRANDE BLVD.
TYLER, TEXAS 75703
(903) 534-0174
TBPLS FIRM REGISTRATION NO. 10025700

ALL BEARINGS AND DISTANCES ARE GRID ARE BASED ON THE TEXAS COORDINATE SYSTEM, CENTRAL ZONE (NAD 1927). UNITS ARE US SURVEY FEET

THE INFORMATION SHOWN HEREON IS INTENDED FOR THE SOLE USE OF APEX NATURAL GAS, LLC. THIS PLAT DOES NOT REPRESENT A BOUNDARY SURVEY. ALL TITLE INFORMATION WAS PROVIDED BY APEX NATURAL GAS, LLC.

I, THE UNDERSIGNED, DO HEREBY CERTIFY THAT THIS PLAT IS TRUE AND CORRECT TO THE BEST OF MY KNOWLEDGE AND BELIEF.

BY:  AUGUST 3, 2026

S. W. SPRAY
REGISTERED PROFESSIONAL LAND SURVEYOR
STATE OF TEXAS NO. 6292

"NORWOOD" QUADRANGLE,
SITUATED SOUTHWEST 4.7 MILES
FROM THE TOWN OF SAN AUGUSTINE, TX.

LEGEND

UNIT OUTLINE —————

SURVEY LINE —————

PERPENDICULAR TO WELL = P.T.W.

0' 750' 1,500' 3,000'

SCALE: 1" = 1,500'

APEX NATURAL GAS, LLC

WELL LOCATION PLAT FOR THE
POOL A 1HB
SAN AUGUSTINE COUNTY, TEXAS

SCALE: 1" = 1,500'

DRAWN BY: S.W.S.

FILE: T250388/POOL A 1HB