


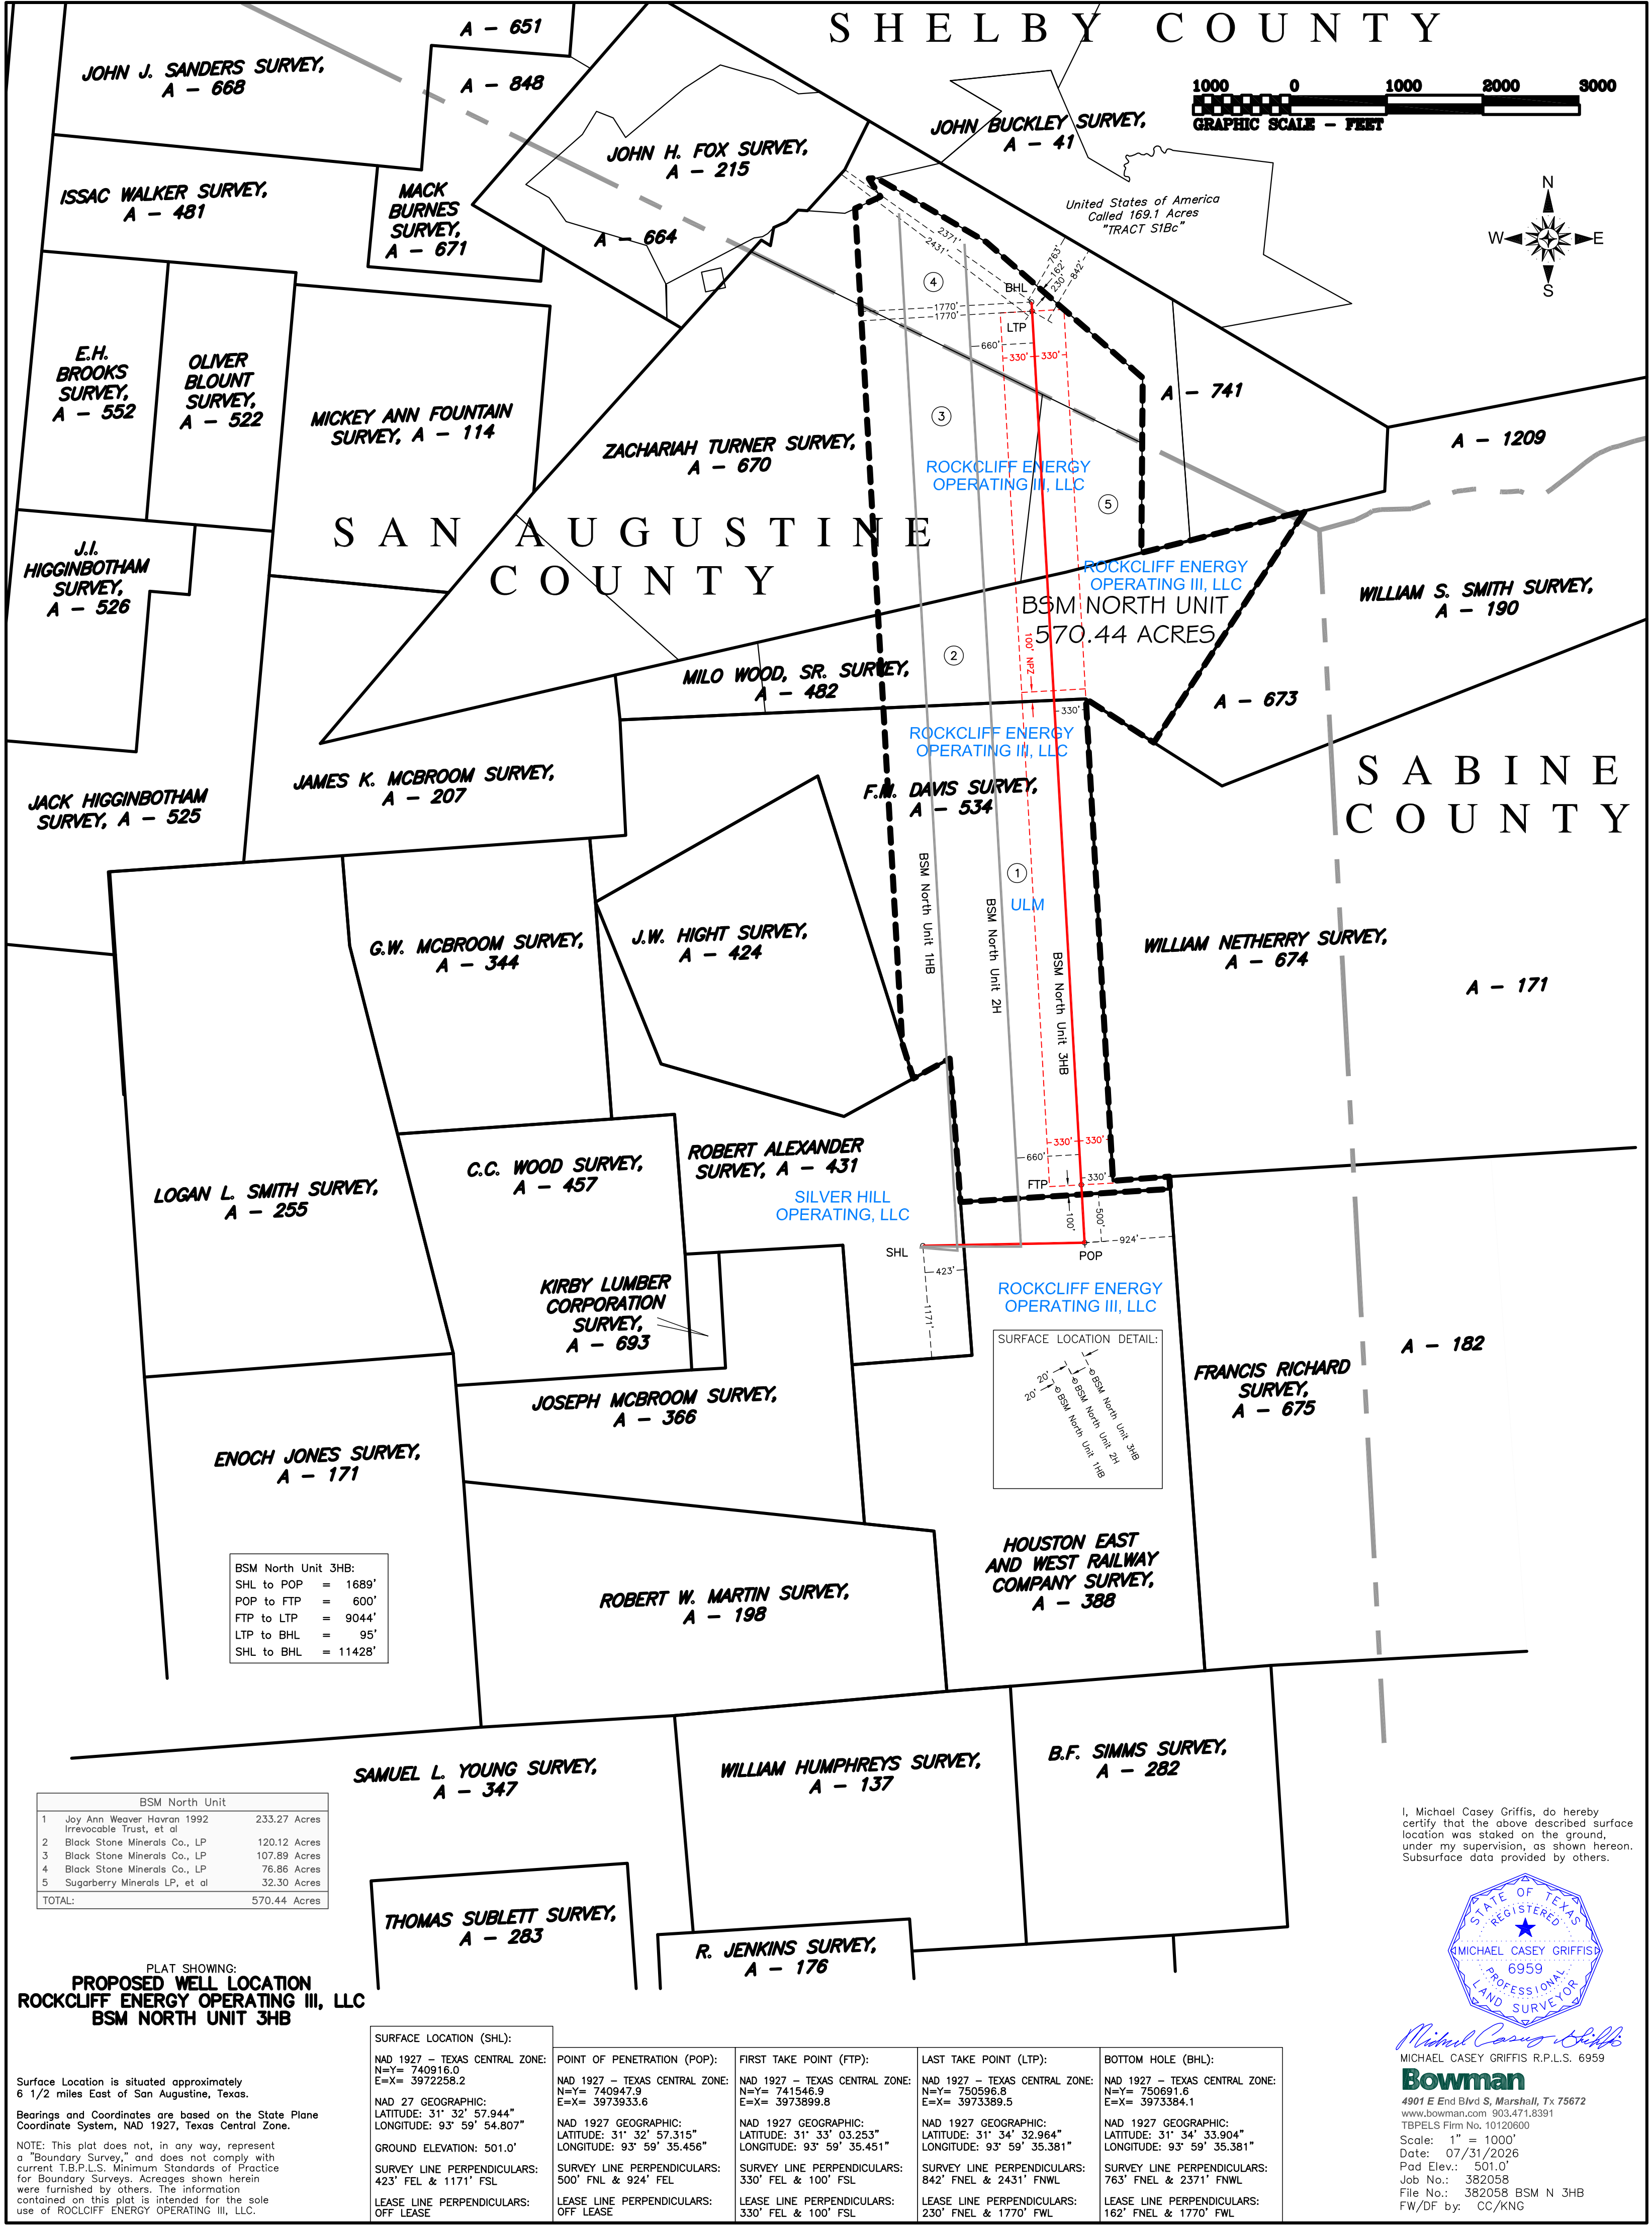

BSM North Unit		
1	Joy Ann Weaver Havran 1992 Irrevocable Trust, et al	233.27 Acres
2	Black Stone Minerals Co., LP	120.12 Acres
3	Black Stone Minerals Co., LP	107.89 Acres
4	Black Stone Minerals Co., LP	76.86 Acres
5	Sugarberry Minerals LP, et al	32.30 Acres
TOTAL:		570.44 Acres

PLAT SHOWING:
PROPOSED WELL LOCATION
ROCKCLIFF ENERGY OPERATING III, LLC
BSM NORTH UNIT 3HB

Surface Location is situated approximately 6 1/2 miles East of San Augustine, Texas.

Bearings and Coordinates are based on the State Plane Coordinate System, NAD 1927, Texas Central Zone.

NOTE: This plat does not, in any way, represent a "Boundary Survey," and does not comply with current T.B.P.L.S. Minimum Standards of Practice for Boundary Surveys. Acreages shown herein were furnished by others. The information contained on this plat is intended for the sole use of ROCKCLIFF ENERGY OPERATING III, LLC.

SURFACE LOCATION (SHL):
NAD 1927 - TEXAS CENTRAL ZONE:
N=Y= 740916.0
E=X= 3972258.2

NAD 27 GEOGRAPHIC:
LATITUDE: 31° 32' 57.944"
LONGITUDE: 93° 59' 54.807"

GROUND ELEVATION: 501.0'

SURVEY LINE PERPENDICULARS:
423' FEL & 1171' FSL

LEASE LINE PERPENDICULARS:
OFF LEASE

POINT OF PENETRATION (POP):
NAD 1927 - TEXAS CENTRAL ZONE:
N=Y= 740947.9
E=X= 3973933.6

NAD 1927 GEOGRAPHIC:
LATITUDE: 31° 32' 57.315"
LONGITUDE: 93° 59' 35.456"

SURVEY LINE PERPENDICULARS:
500' FNL & 924' FEL

LEASE LINE PERPENDICULARS:
OFF LEASE

FIRST TAKE POINT (FTP):
NAD 1927 - TEXAS CENTRAL ZONE:
N=Y= 741546.9
E=X= 3973899.8

NAD 1927 GEOGRAPHIC:
LATITUDE: 31° 33' 03.253"
LONGITUDE: 93° 59' 35.451"

SURVEY LINE PERPENDICULARS:
330' FEL & 100' FSL

LEASE LINE PERPENDICULARS:
330' FEL & 100' FSL

LAST TAKE POINT (LTP):
NAD 1927 - TEXAS CENTRAL ZONE:
N=Y= 750596.8
E=X= 3973389.5

NAD 1927 GEOGRAPHIC:
LATITUDE: 31° 34' 32.964"
LONGITUDE: 93° 59' 35.381"

SURVEY LINE PERPENDICULARS:
842' FNL & 2431' FNL

LEASE LINE PERPENDICULARS:
230' FNL & 1770' FNL

BOTTOM HOLE (BHL):
NAD 1927 - TEXAS CENTRAL ZONE:
N=Y= 750691.6
E=X= 3973384.1

NAD 1927 GEOGRAPHIC:
LATITUDE: 31° 34' 33.904"
LONGITUDE: 93° 59' 35.381"

SURVEY LINE PERPENDICULARS:
763' FNL & 2371' FNL

LEASE LINE PERPENDICULARS:
162' FNL & 1770' FNL

I, Michael Casey Griffis, do hereby certify that the above described surface location was staked on the ground, under my supervision, as shown hereon. Subsurface data provided by others.



Michael Casey Griffis
MICHAEL CASEY GRIFFIS R.P.L.S. 6959
Bowman
4901 E End Blvd S, Marshall, Tx 75672
www.bowman.com 903.471.8391
TBPELS Firm No. 10120600
Scale: 1" = 1000'
Date: 07/31/2026
Pad Elev.: 501.0'
Job No.: 382058
File No.: 382058 BSM N 3HB
FW/DF by: CC/KNG