


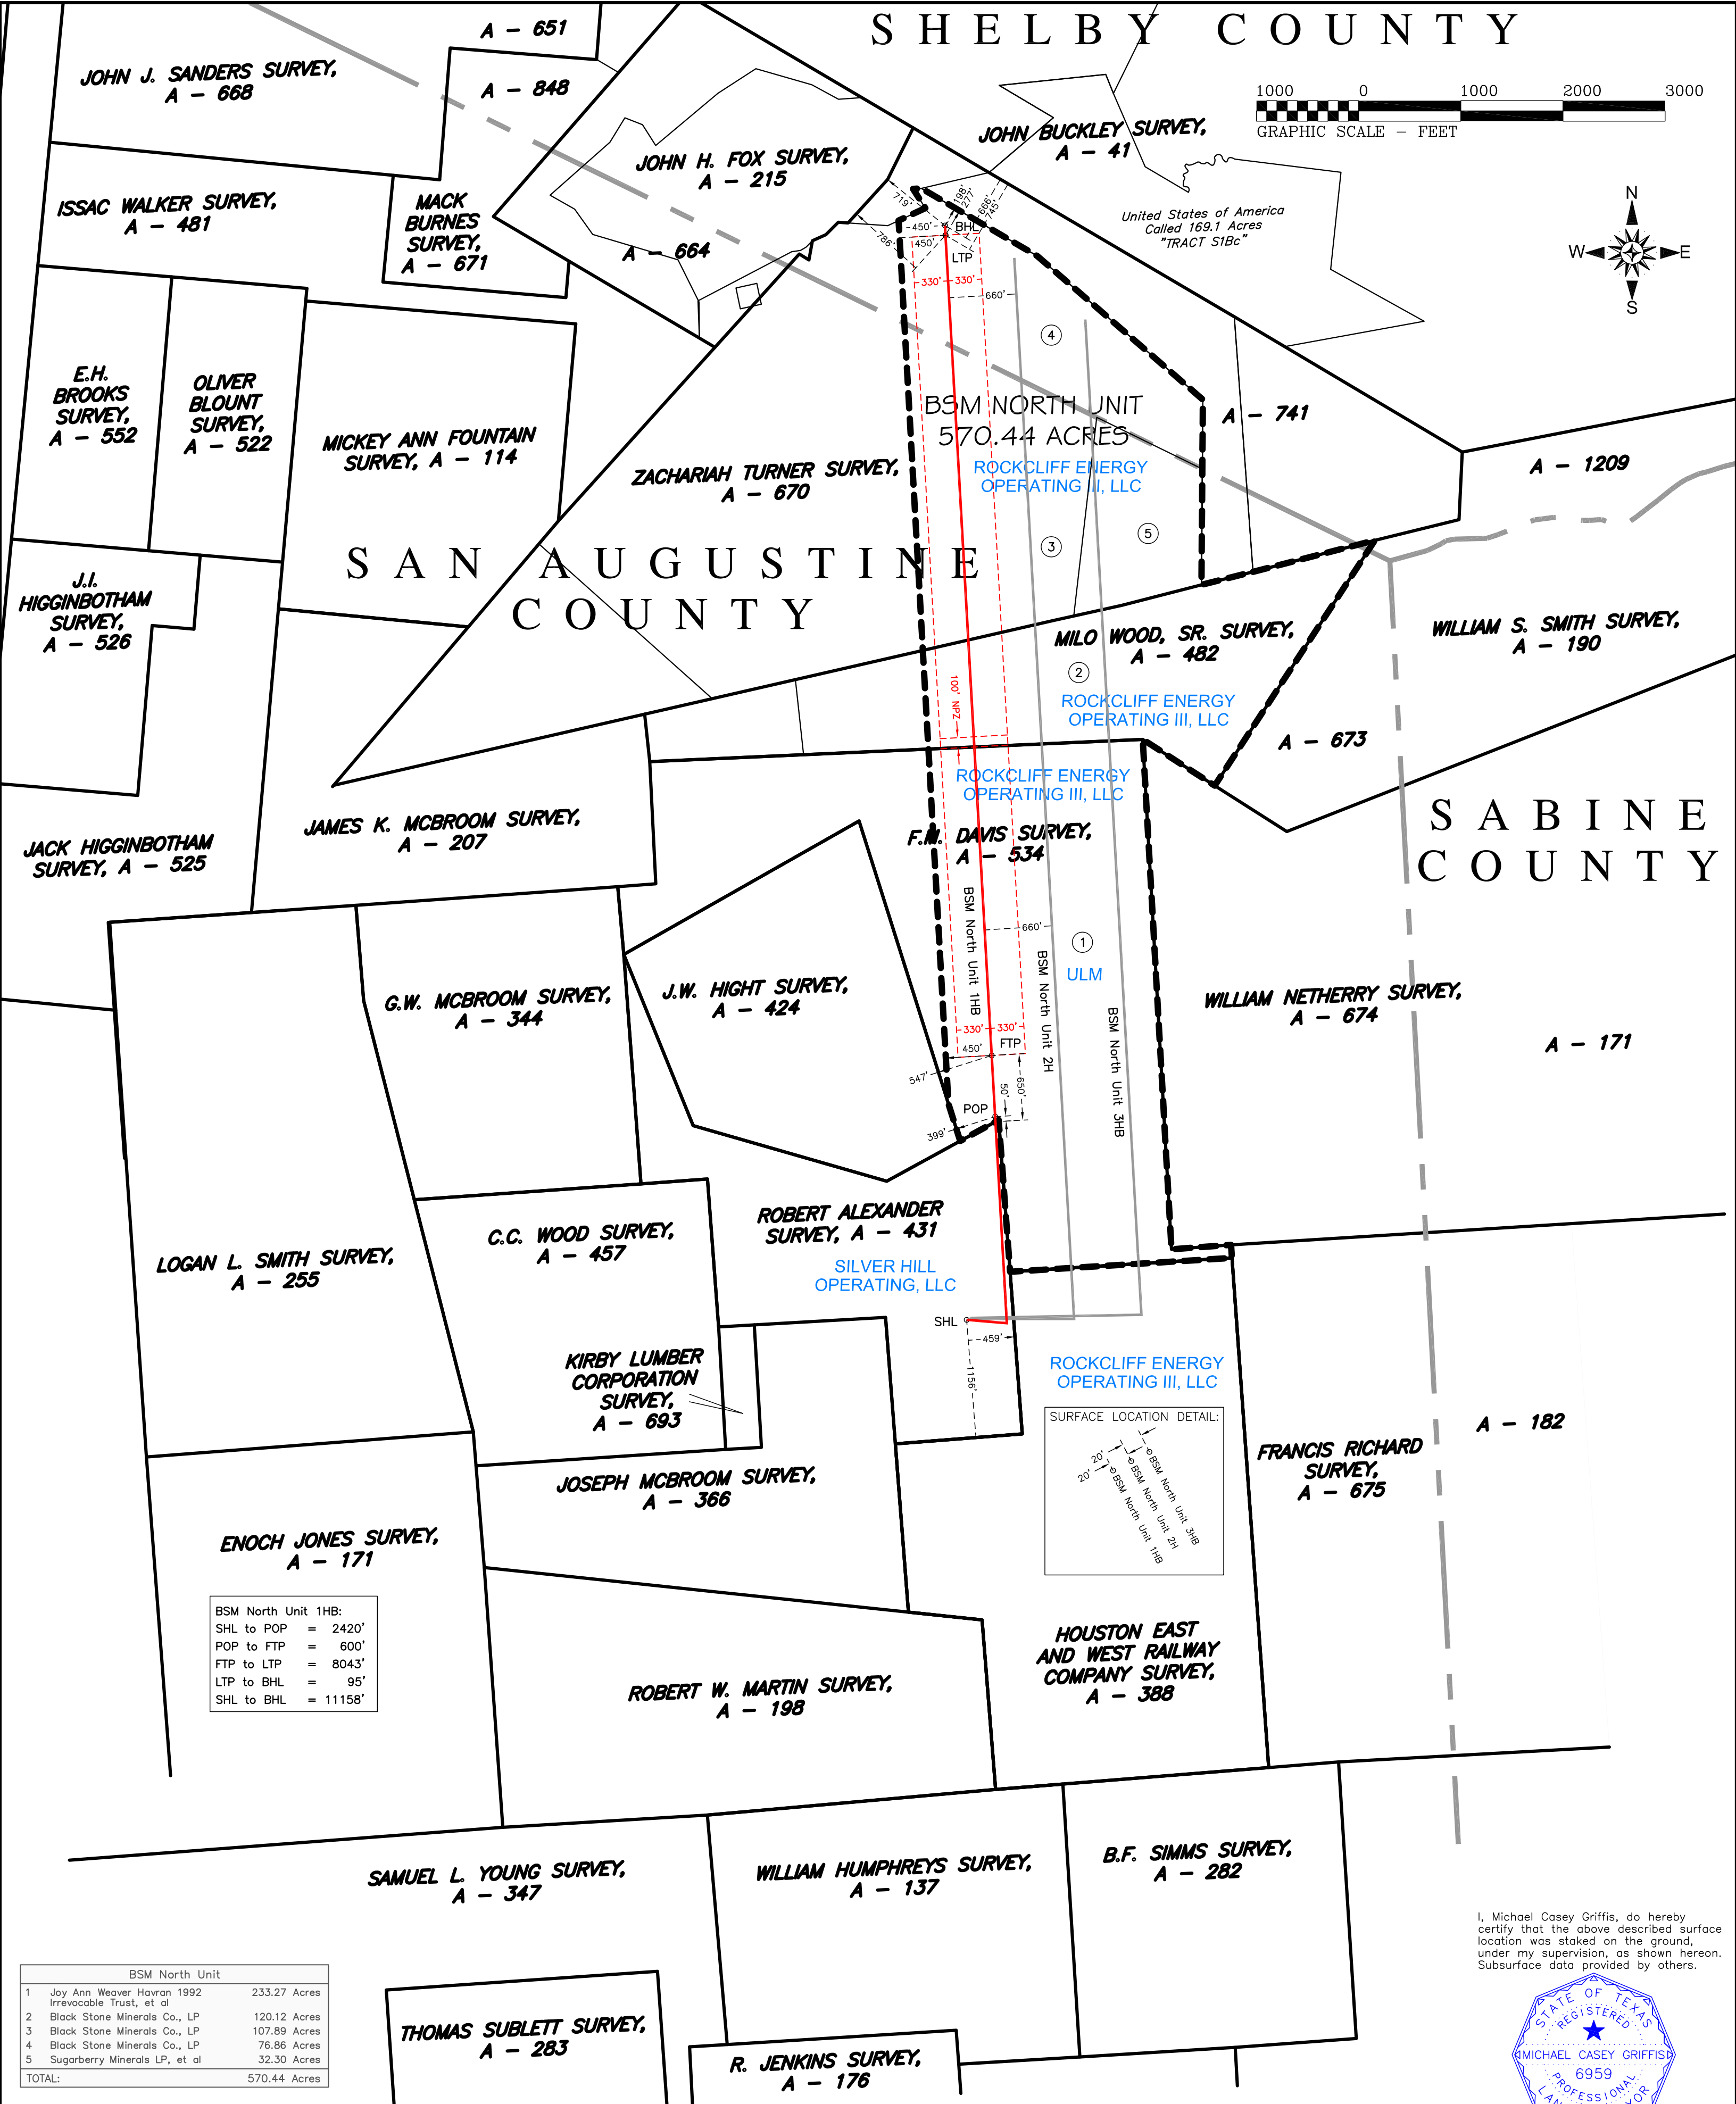

PLAT SHOWING:  
**PROPOSED WELL LOCATION**  
**ROCKCLIFF ENERGY OPERATING III, LLC**  
**BSM NORTH UNIT 1HB**

Surface Location is situated approximately  
6 1/2 miles East of San Augustine, Texas.

Bearings and Coordinates are based on the State Plane  
Coordinate System, NAD 1927, Texas Central Zone.

**SURFACE LOCATION (SHL):**  
NAD 1927 - TEXAS CENTRAL ZONE:  
N=740897.7  
E=X= 3972222.7  
NAD 27 GEOGRAPHIC:  
LATITUDE: 31° 32' 57.784"  
LONGITUDE: 93° 59' 55.230"  
GROUND ELEVATION: 501.0'  
SURVEY LINE PERPENDICULARS:  
459' FEL & 1156' FSL  
LEASE LINE PERPENDICULARS:  
OFF LEASE

**POINT OF PENETRATION (POP):**  
NAD 1927 - TEXAS CENTRAL ZONE:  
N=Y= 742887.5  
E=X= 3972502.1  
NAD 1927 GEOGRAPHIC:  
LATITUDE: 31° 33' 17.288"  
LONGITUDE: 93° 59' 50.697"  
SURVEY LINE PERPENDICULARS:  
50' FSL & 399' FWL  
LEASE LINE PERPENDICULARS:  
50' FSL & 399' FWL

**FIRST TAKE POINT (FTP):**  
NAD 1927 - TEXAS CENTRAL ZONE:  
N=Y= 743466.6  
E=X= 3972468.3  
NAD 1927 GEOGRAPHIC:  
LATITUDE: 31° 33' 23.226"  
LONGITUDE: 93° 59' 50.692"  
SURVEY LINE PERPENDICULARS:  
547' FWL & 650' FSL  
LEASE LINE PERPENDICULARS:  
450' FWL & 650' FSL

**LAST TAKE POINT (LTP):**  
NAD 1927 - TEXAS CENTRAL ZONE:  
N=Y= 751516.9  
E=X= 3972015.5  
NAD 1927 GEOGRAPHIC:  
LATITUDE: 31° 34' 42.830"  
LONGITUDE: 93° 59' 50.634"  
SURVEY LINE PERPENDICULARS:  
745' FNEL & 786' FNWL  
LEASE LINE PERPENDICULARS:  
277' FNEL & 450' FWL

**BOTTOM HOLE (BHL):**  
NAD 1927 - TEXAS CENTRAL ZONE:  
N=Y= 751811.7  
E=X= 3972010.1  
NAD 1927 GEOGRAPHIC:  
LATITUDE: 31° 34' 43.770"  
LONGITUDE: 93° 59' 50.634"  
SURVEY LINE PERPENDICULARS:  
666' FNEL & 719' FNWL  
LEASE LINE PERPENDICULARS:  
198' FNEL & 450' FWL

I, Michael Casey Griffis, do hereby  
certify that the above described surface  
location was staked on the ground,  
under my supervision, as shown hereon.  
Subsurface data provided by others.



*Michael Casey Griffis*  
MICHAEL CASEY GRIFFIS R.P.L.S. 6959  
**Bowman**  
4901 E End Blvd S, Marshall, Tx 75672  
www.bowman.com 903.471.8391  
TBPELS Firm No. 10120600  
Scale: 1" = 1000'  
Date: 08/05/2026  
Pad Elev.: 501.0'  
Job No.: 382058  
File No.: 382058 BSM N 1HB  
FW/DF by: CC/KNG