1000 Ledgelawn Drive
Conway, Arkansas 72034

Crafton Tull
surveying


501.328.3316 t 501.328.3325 f
www.craftontull.com

NOTE: * DENOTES TRACTS WITH UNLEASED MINERAL INTEREST (ULM) AND/OR 3RD PARTY WORKING INTEREST NOT SUBJECT TO AN OPERATING AGREEMENT

SHELBY COUNTY, TEXAS

NOTE: S.H.L. APPROXIMATE LOCATION IS **3.9 MILES NORTH** OF EAST HAMILTON, TEXAS

S.H.L. LOCATED IN W. HOPSON SURVEY, A - 375 AND
B.H.L. LOCATED IN S. OBANNON SURVEY, A - 536.

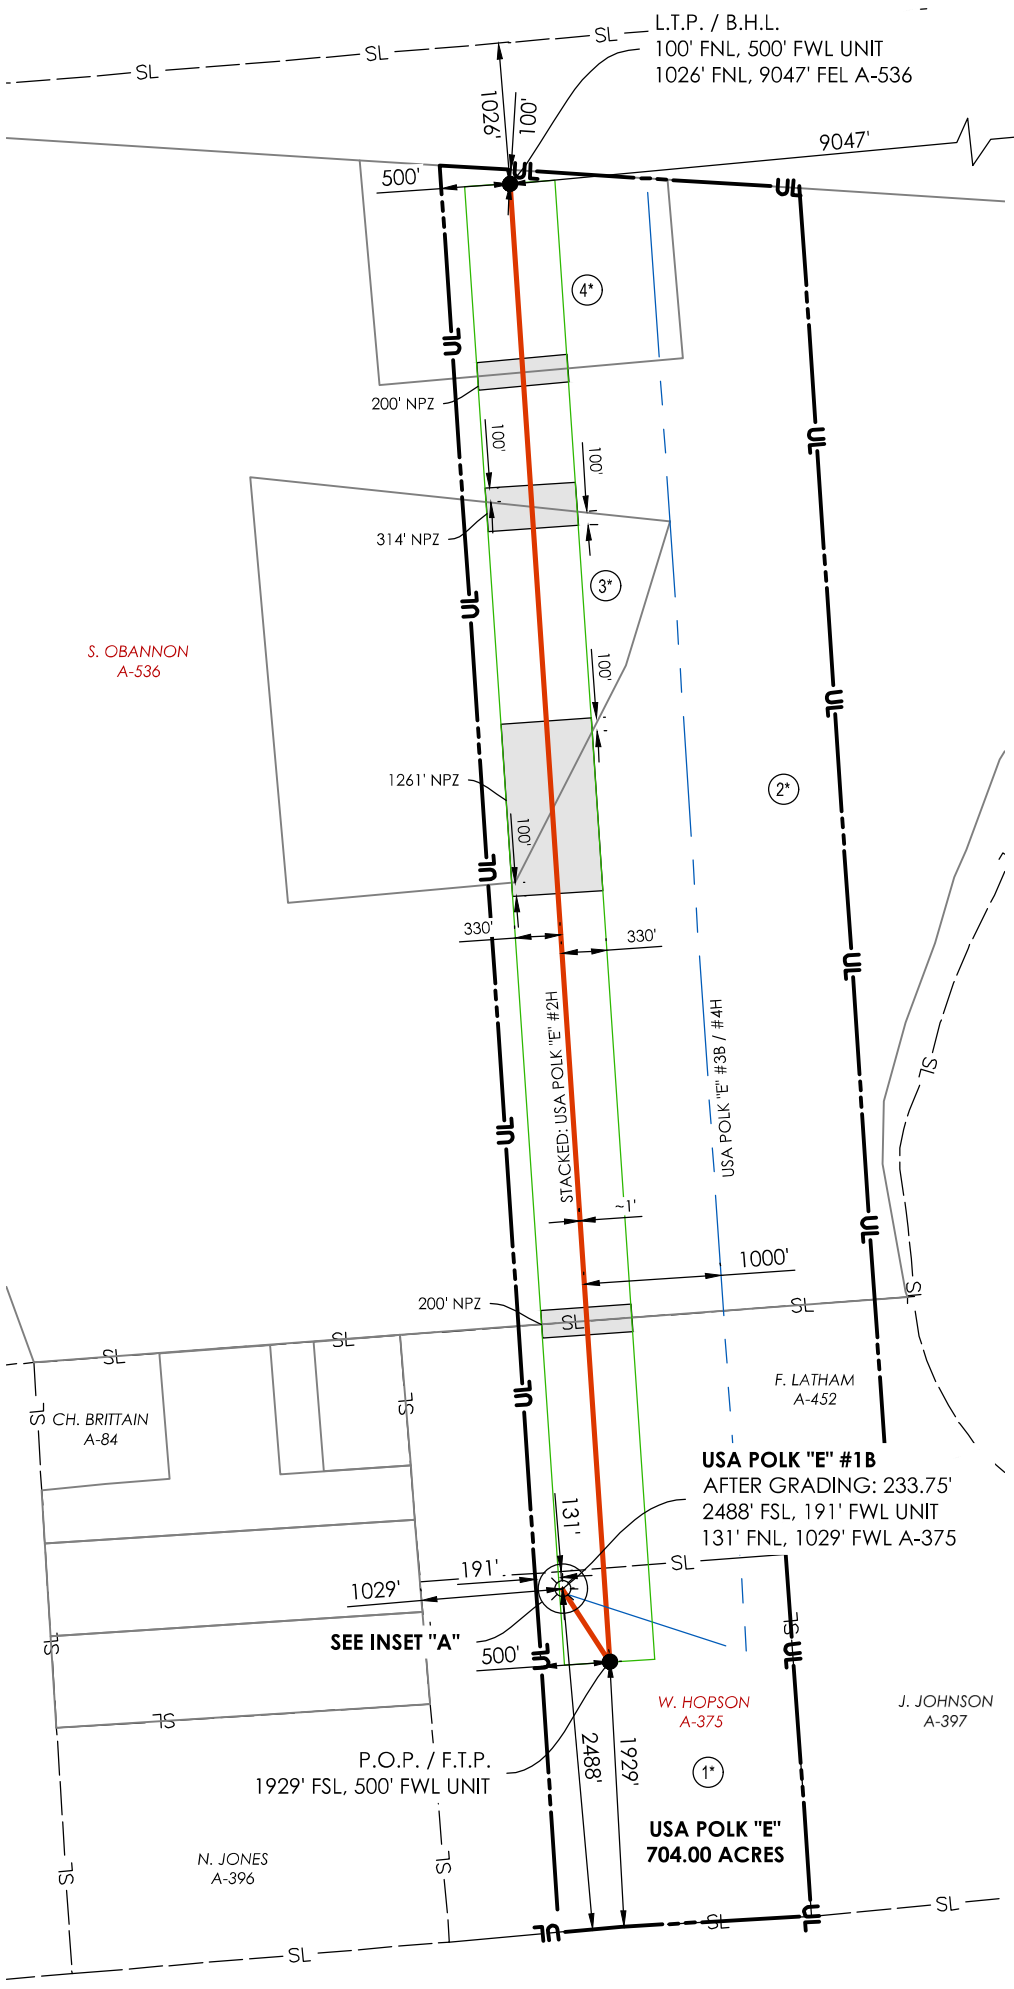

LEGEND

UL	LEASE LINE
	PROPOSED WELL PATH
	NEAREST WELL PATH
SL	SURVEY LINE
	OWNERSHIP LINE
S.H.L.	SURFACE HOLE LOCATION
P.O.P.	POINT OF PENETRATION
F.T.P.	FIRST TAKE POINT
T.P.	TURNING POINT
L.T.P.	LAST TAKE POINT
B.H.L.	BOTTOM HOLE LOCATION
D.H.	DRAIN HOLE
	660' BOUNDARY BOX
	NO PERF ZONE (N.P.Z.)

GRID NORTH (NAD 83)
TEXAS - CENTRAL ZONE

USA POLK "E"


TRACT	PARTICIPANT	ACREAGE
1*	UNITED STATES OF AMERICA - TXNM 108071	207.65
2*	UNITED STATES OF AMERICA - TXNM 108071	383.86
3*	BAYOU BLEU, ET AL	58.00
4*	W.I. DAVIS, ET AL	54.49
TOTAL		704.00

STATE OF TEXAS
REGISTERED
BRADLEY G RUSSELL
6349
PROFESSIONAL
LAND SURVEYOR

X
8/6/2026

CONTACT INFORMATION:
Bradley G. Russell
Crafton Tull (10193715)
1000 Ledgelawn Dr.
Conway, AR 72034

INSET "A" (N.T.S.)

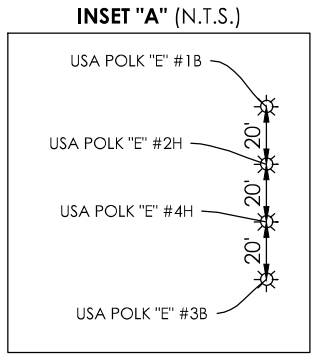

WELL BORE POSITIONS

REFERENCE	LAT. **(NAD 83)**	LONG. **(NAD 83)**	NORTHING **(NAD 83)**	EASTING **(NAD 83)**
S.H.L.	31.65815719	-93.83497389	10625859.40	4317362.50
P.O.P. / F.T.P.	31.65664293	-93.83396600	10625327.82	4317707.73
L.T.P. / B.H.L.	31.68633593	-93.83427871	10636104.96	4316979.91

WELL BORE POSITIONS

REFERENCE	LAT. **(NAD 27)**	LONG. **(NAD 27)**	NORTHING **(NAD 27)**	EASTING **(NAD 27)**
S.H.L.	31.65798242	-93.83478708	783275.31	4020883.57
P.O.P. / F.T.P.	31.65646812	-93.83377923	782743.73	4021228.80
L.T.P. / B.H.L.	31.68616204	-93.83409181	793520.85	4020501.00

WELL PATH DATA

REF.	BEARING	DISTANCE
SHL TO POP/FTP	S 33°00'05" E	633.85'
POP/FTP TO LTP/BHL	N 03°51'49" W	10,801.68'

WELL PATH DATA

REF.	LEASE/UNIT CALLS	SURVEY LINE CALLS (±)
S.H.L.	2488' FSL, 191' FWL	131' FNL, 1029' FWL
P.O.P. / F.T.P.	1929' FSL, 500' FWL	
L.T.P. / B.H.L.	100' FNL, 500' FWL	1026' FNL, 9047' FEL

1400' 700' 0 1400'

NOTE: THIS IS NOT A BOUNDARY SURVEY AS DEFINED BY STATE OR LOCAL LAWS. THE BOUNDARY AND DRILLING UNIT LINES SHOWN HEREON ARE ONLY APPROXIMATE BASED ON INFORMATION SUPPLIED TO THE SURVEYOR BY THE CLIENT. ALTHOUGH THEY ARE PLACED AS ACCURATELY AS POSSIBLE BASED ON AVAILABLE INFORMATION, NO FIELD SURVEY WAS CONDUCTED BY THE SURVEYOR TO VERIFY THE ACCURACY OF THE BOUNDARY LINES SHOWN. ONLY THE SURFACE HOLE POSITIONS WERE FIELD LOCATED BY THE SURVEYOR.

GENERAL NOTES
1. THE LOCATIONS OF UNDERGROUND UTILITIES AS SHOWN HEREON ARE BASED ON REASONABLE VISUAL OBSERVATION. LOCATIONS OF UNDERGROUND UTILITIES/ STRUCTURES MAY VARY FROM LOCATIONS SHOWN HEREIN. ADDITIONAL BURIED UTILITIES/ STRUCTURES MAY BE ENCOUNTERED. NO EXCAVATIONS WERE MADE DURING THE PROGRESS OF THIS SURVEY TO LOCATE BURIED UTILITIES/ STRUCTURES. BEFORE EXCAVATIONS ARE BEGUN, THE OFFICES OF THE VARIOUS UTILITIES SERVICING THIS AREA SHOULD BE CONTACTED FOR THEIR UTILITY LOCATION.
2. PROJECT COORDINATE SYSTEM: TEXAS STATE PLANE, CENTRAL ZONE, NAD'83, U.S. FEET AS DETERMINED BY GPS OBSERVATION.
3. S.H.L. ELEVATIONS SHOWN HEREON ARE PRIOR TO CONSTRUCTION. FINISHED ELEVATIONS MAY VARY.
4. THE SURVEY LINES SHOWN HEREON FROM THE RAILROAD COMMISSION GIS DATABASE OR STATE OF TEXAS DATA, AND MAY NOT REFLECT THE ACTUAL ABSTRACT LINE AS SURVEYED ON THE GROUND.

REVISION	
1	NAME CHX 06/10/26
2	BHL FEL 08/06/26

SILVER HILL ENERGY OPERATING, LLC

USA POLK "E" #1B
S.H.L. IN W. HOPSON, A-375, B.H.L. IN S. OBANNON, A-536
SHELBY COUNTY, TEXAS

SCALE: 1" =	1400'	CHECKED BY:	LD
PLOT DATE:	08/06/2026	DRAWN BY:	BR
APPROVED BY:			NPE
SHEET NO.:	1	OF	1

G:\8915 SILVER HILL ENERGY PARTNERS\ENERGY\8915SV0062 POLK PAD\POLK PAD 051826.DWG 8/6/2026 8:50:48 AM BR1169