



1000 LedgeLawn Drive  
Conway, Arkansas 72034


501.328.3316 t 501.328.3325 f  
www.craftontull.com

NOTE: \* DENOTES TRACTS WITH UNLEASED MINERAL INTEREST (ULM)  
AND/OR 3RD PARTY WORKING INTEREST NOT SUBJECT TO AN  
OPERATING AGREEMENT

SHELBY COUNTY, TEXAS

NOTE: S.H.L. APPROXIMATE LOCATION IS 3.9 MILES NORTH  
OF EAST HAMILTON, TEXAS

S.H.L. LOCATED IN W. HOPSON SURVEY, A - 375 AND  
B.H.L. LOCATED IN S. OBANNON SURVEY, A - 536.

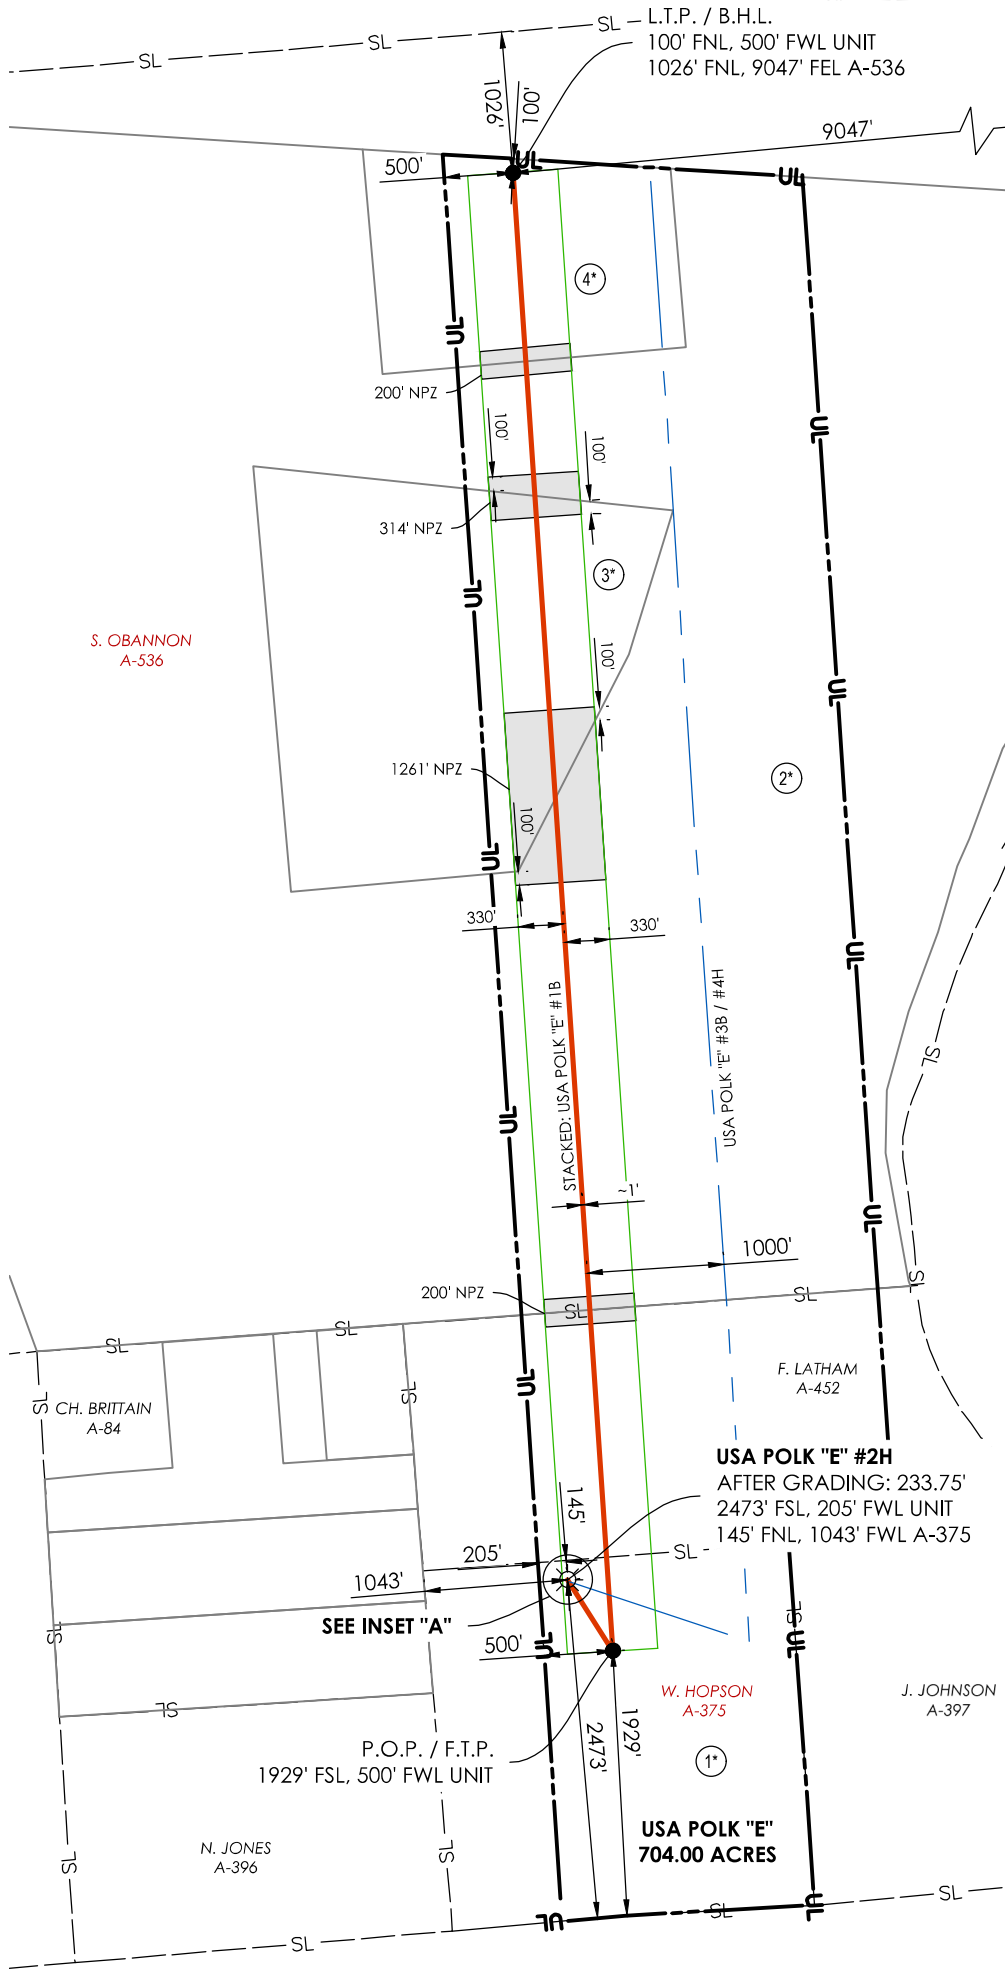

| LEGEND |                       |
|--------|-----------------------|
|        | LEASE LINE            |
|        | PROPOSED WELL PATH    |
|        | NEAREST WELL PATH     |
|        | SURVEY LINE           |
|        | OWNERSHIP LINE        |
|        | SURFACE HOLE LOCATION |
|        | POINT OF PENETRATION  |
|        | FIRST TAKE POINT      |
|        | TURNING POINT         |
|        | LAST TAKE POINT       |
|        | BOTTOM HOLE LOCATION  |
|        | DRAIN HOLE            |
|        | 660' BOUNDARY BOX     |
|        | NO PERF ZONE (N.P.Z.) |

GRID NORTH (NAD 83)  
TEXAS - CENTRAL ZONE

USA POLK "E"

| TRACT | PARTICIPANT                            | ACREAGE |
|-------|----------------------------------------|---------|
| 1*    | UNITED STATES OF AMERICA - TXNM 108071 | 207.65  |
| 2*    | UNITED STATES OF AMERICA - TXNM 108071 | 383.86  |
| 3*    | BAYOU BLEU, ET AL                      | 58.00   |
| 4*    | W.I. DAVIS, ET AL                      | 54.49   |
| TOTAL |                                        | 704.00  |



CONTACT INFORMATION:  
Bradley G. Russell  
Crafton Tull (10193715)  
1000 LedgeLawn Dr.  
Conway, AR 72034

WELL BORE POSITIONS

| REFERENCE       | LAT. (NAD 83) | LONG. (NAD 83) | NORTHING (NAD 83) | EASTING (NAD 83) |
|-----------------|---------------|----------------|-------------------|------------------|
| S.H.L.          | 31.65811856   | -93.83492824   | 10625846.20       | 4317377.50       |
| P.O.P. / F.T.P. | 31.65664293   | -93.83396600   | 10625327.82       | 4317707.73       |
| L.T.P. / B.H.L. | 31.68633593   | -93.83427871   | 10636104.96       | 4316979.91       |

WELL BORE POSITIONS

| REFERENCE       | LAT. (NAD 27) | LONG. (NAD 27) | NORTHING (NAD 27) | EASTING (NAD 27) |
|-----------------|---------------|----------------|-------------------|------------------|
| S.H.L.          | 31.65794379   | -93.83474144   | 783262.11         | 4020898.57       |
| P.O.P. / F.T.P. | 31.65646812   | -93.83377923   | 782743.73         | 4021228.80       |
| L.T.P. / B.H.L. | 31.68616204   | -93.83409181   | 793520.85         | 4020501.00       |



WELL PATH DATA

| REF.               | BEARING       | DISTANCE   |
|--------------------|---------------|------------|
| SHL TO POP/FTP     | S 32°29'56" E | 614.63'    |
| POP/FTP TO LTP/BHL | N 03°51'49" W | 10,801.68' |

WELL PATH DATA

| REF.            | LEASE/UNIT CALLS    | SURVEY LINE CALLS (±) |
|-----------------|---------------------|-----------------------|
| S.H.L.          | 2473' FSL, 205' FWL | 145' FNL, 1043' FWL   |
| P.O.P. / F.T.P. | 1929' FSL, 500' FWL |                       |
| L.T.P. / B.H.L. | 100' FNL, 500' FWL  | 1026' FNL, 9047' FEL  |

INSET "A" (N.T.S.)

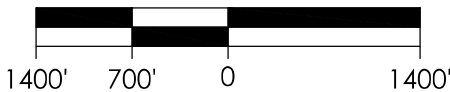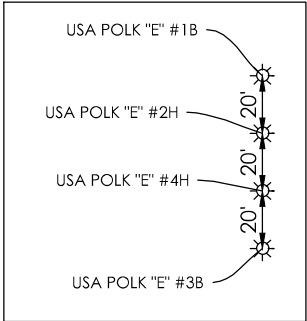

NOTE: THIS IS NOT A BOUNDARY SURVEY AS DEFINED BY STATE OR  
LOCAL LAWS. THE BOUNDARY AND DRILLING UNIT LINES SHOWN  
HEREON ARE ONLY APPROXIMATE BASED ON INFORMATION SUPPLIED  
TO THE SURVEYOR BY THE CLIENT. ALTHOUGH THEY ARE PLACED AS  
ACCURATELY AS POSSIBLE BASED ON AVAILABLE INFORMATION, NO  
FIELD SURVEY WAS CONDUCTED BY THE SURVEYOR TO VERIFY THE  
ACCURACY OF THE BOUNDARY LINES SHOWN. ONLY THE SURFACE HOLE  
POSITIONS WERE FIELD LOCATED BY THE SURVEYOR.

GENERAL NOTES

- THE LOCATIONS OF UNDERGROUND UTILITIES AS SHOWN HEREON ARE BASED ON REASONABLE VISUAL OBSERVATION. LOCATIONS OF UNDERGROUND UTILITIES/ STRUCTURES MAY VARY FROM LOCATIONS SHOWN HEREIN. ADDITIONAL BURIED UTILITIES/ STRUCTURES MAY BE ENCOUNTERED. NO EXCAVATIONS WERE MADE DURING THE PROGRESS OF THIS SURVEY TO LOCATE BURIED UTILITIES/ STRUCTURES. BEFORE EXCAVATIONS ARE BEGUN, THE OFFICES OF THE VARIOUS UTILITIES SERVICING THIS AREA SHOULD BE CONTACTED FOR THEIR UTILITY LOCATION.
- PROJECT COORDINATE SYSTEM: TEXAS STATE PLANE, CENTRAL ZONE, NAD83, U.S. FEET AS DETERMINED BY GPS OBSERVATION.
- S.H.L. ELEVATIONS SHOWN HEREON ARE PRIOR TO CONSTRUCTION. FINISHED ELEVATIONS MAY VARY.
- THE SURVEY LINES SHOWN HEREON FROM THE RAILROAD COMMISSION GIS DATABASE OR STATE OF TEXAS DATA, AND MAY NOT REFLECT THE ACTUAL ABSTRACT LINE AS SURVEYED ON THE GROUND.

| REVISION |                   |
|----------|-------------------|
| 1        | NAME CHX 06/10/26 |
| 2        | BHL FEL 08/06/26  |
|          |                   |
|          |                   |
|          |                   |
|          |                   |

SILVER HILL ENERGY OPERATING, LLC

USA POLK "E" #2H  
S.H.L. IN W. HOPSON, A-375, B.H.L. IN S. OBANNON, A-536  
SHELBY COUNTY, TEXAS

|                       |                |                   |
|-----------------------|----------------|-------------------|
| SCALE: 1" = 1400'     | CHECKED BY: LD | APPROVED BY: NPE  |
| PLOT DATE: 08/06/2026 | DRAWN BY: BR   | SHEET NO.: 1 OF 1 |