


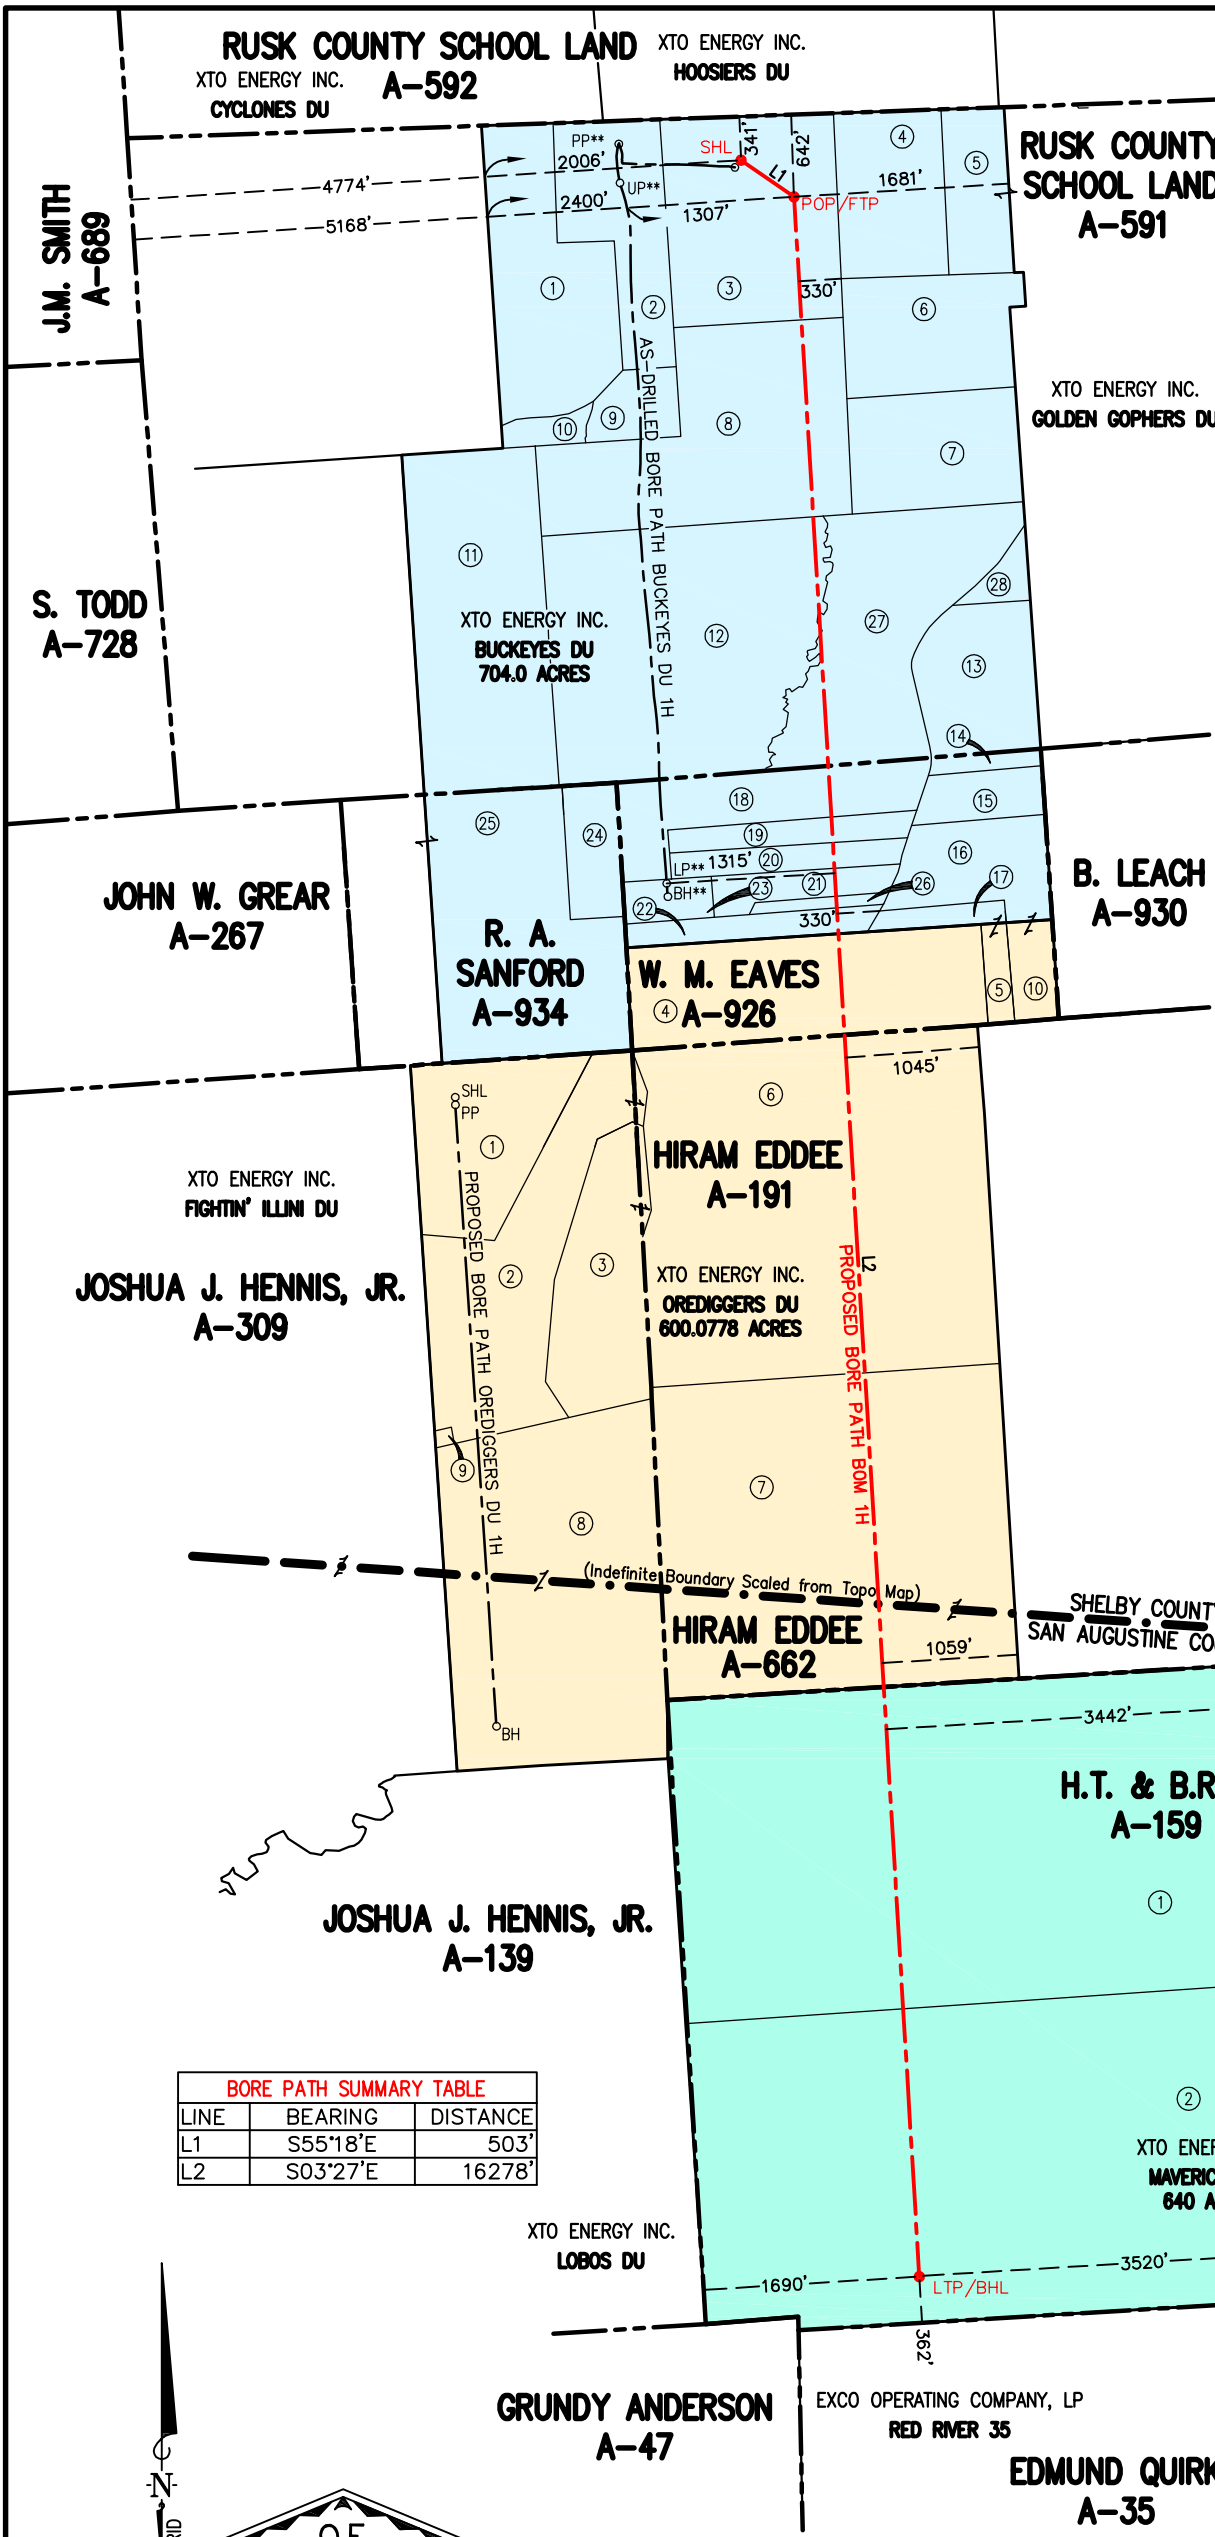

Buckeyes DU Unit Tract Information			
Tract No.	Acreage	Ownership	Vol./Pg.
1	39.5 Ac.	Brealon Sanford, Jr.	360/285
2	27.4 Ac.	Zap Minerals, L.P.	198/510
3	51 Ac.	Zap Minerals, L.P.	198/510
4	25 Ac.	Sharon Bridges, et al	458/296
5	(14.8314 Ac.)	Sharon Bridges, et al	458/296
6	(28.3 Ac.)	Frank Lewis Pearce, Jr., et al	458/296
7	(26.8 Ac.)	Tom M. Jones & Lee Andrew Jones, II	458/296
8	62.5 Ac.	Baptist Foundation of Texas	458/296
9	10 Ac.	Baptist Foundation of Texas	458/296
10	3 Ac.	Baptist Foundation of Texas	458/296
11	(66.36 Ac.)	Baptist Foundation of Texas	458/296
12	90 Ac.	BP America Production Company	132/171
13	(22.24 Ac.)	Mr. George Clark Sr., et al	994/456
14	2.6266 Ac.	Lois Eaves, et al	163/534
15	8.5165 Ac.	Tom Kimbro et ux	502/422
16	(18.9045 Ac.)	Magdalene Lovell Adams, et al	533/223
17	(3.965 Ac.)	Bill F. Griffin, Jr. et ux	502/422
18	25.5495 Ac.	The E. H. & B.G. Applequist Living Trust	598/581
19	8.5165 Ac.	The E. H. & B.G. Applequist Living Trust	547/187
20	8.5165 Ac.	Mildred Pierce et vir	547/187
21	7.994 Ac.	Renea Lovell Sanders	751/422
22	8.5165 Ac.	Verl Windham et ux	751/38
23	5.2532 Ac.	Annette F. Eaves, et al	895/139
24	10.3547 Ac.	Baptist Foundation of Texas	502/422
25	(60.4261 Ac.)	Baptist Foundation of Texas	458/296
26	2.169 Ac.	Donnie Glynn Dickerson, Jr., et al	104/613
27	(62.42 Ac.)	Tom Jones, et al	965/516
28	(3.34 Ac.)	George Clark, Jr., et al	797/61


Orediggers DU Unit Tract Information			
Tract No.	Acreage	Ownership	Vol./Pg.
1	(31.69 Ac.)	Linda E. Oliver Noble, et al	664/702
2	(49.94 Ac.)	Marvin Willis Oliver, et al	664/699
3	31.45 Ac.	Linda E. Oliver Noble, et al	698/567
4	50.8 Ac.	Hugh W. Curfman, et al	252/470
5	(3.676 Ac.)	Bill F. Griffin, Jr. et ux	598/581
6	162.31 Ac.	Murrel Louise Williams, et al	671/11
7	160.0 Ac.	Frank W. Greer, Jr.	34/165
8	(103.51 Ac.)	Benjamin Holman Bright, et al	480/439
9	(0.42 Ac.)	Gertie Leach, et al	403/407
10	(6.2818)	Magdalene Lovell Adams, et al	502/422

Mavericks DU Unit Tract Information			
Tract No.	Acreage	Ownership	Vol./Pg.
1	320 Ac.	Winnie Greer Markle, et al	181/84
2	320 Ac.	Winnie Greer Markle, et al	181/84

BOM 1H	
UNIT	ACRES (CALLED)
BUCKEYES DU	704.0 ACRES
OREDIGGERS DU	600.0778 ACRES
MAVERICKS DU	640 ACRES
TOTAL	1944.0778 ACRES

PRODUCTION LENGTH (FTP TO LTP)	
BUCKEYES DU	5767'
OREDIGGERS DU	5895'
MAVERICKS DU	4616'
TOTAL	16278'

BORE PATH SUMMARY TABLE		
LINE	BEARING	DISTANCE
L1	S55°18'E	503'
L2	S03°27'E	16278'

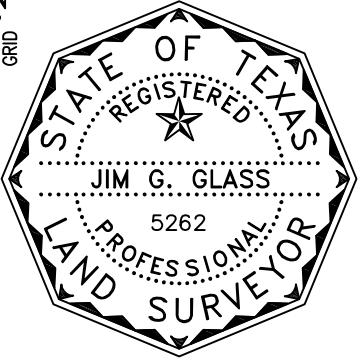

FOR THE EXCLUSIVE USE OF
XTO ENERGY INC.
STATE OF TEXAS - - - COUNTY OF SMITH
I, Jim G. Glass, Registered Professional Land
Surveyor, do hereby certify the above plat to be
true and correct to the best of my knowledge.
Date: July 27, 2026 Bullard, Texas


E.L.S. SURVEYING & MAPPING, INC.
Registered Professional Land Surveyor No. 5262
07-27-202608:44:33:05:00

Location is located approximately
5.9 miles SE of Shelbyville, Texas
"HURSTOWN" Quadrangle
As Drilled information was provided by others

	SURVEY LOCATION	UNIT TIES	ELEV. (NAVD 88)	NAD 27 TEXAS STATE PLANE COORDINATES	NAD 27 GEOGRAPHIC COORDINATES (DD)
SHL	341' FNL 4774' FWL	341' FNL 2006' FWL	448.0'	Y=778,049.53' X=3,917,181.63'	LAT.=31.6598575' LONG.= -94.1684904'
POP/FTP	642' FNL 5168' FWL	642' FNL 1681' FEL	- - -	Y=777,763.10' X=3,917,595.28'	LAT.=31.6590083' LONG.= -94.1672140'
BHL	362' FSL 1690' FWL	362' FSL 1690' FWL	- - -	Y=761,515.08' X=3,918,574.44'	LAT.=31.6142594' LONG.= -94.1669651'

Location is staked from tract lines as evidenced by occupation,
information obtained from the General Land Office and provided
deed records. Distances shown are not intended to be
definitive in establishing actual title boundaries. The deed data,
tract acreages and unit data shown hereon was furnished by
others. This is not a title survey. Vesting documents may not
have been provided. Bearings and distances are based on the
Texas State Plane Coordinate System, N.A.D. 27 (Central Zone)
Derived from GPS Observations.

WELL LOCATION PLAT
XTO ENERGY INC.
BOM 1H
SURVEYS AS SHOWN
SHELBY COUNTY, TEXAS
SAN AUGUSTINE COUNTY, TEXAS
PAGE 1 OF 1

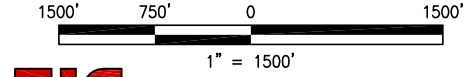

ELSA SURVEYING & MAPPING INC.
TBPELS Firm No. 100327-00
21072 FM 2493 / Bullard, Texas 75757 / 903-581-7759