



GENIO RAMIREZ
SURVEY, A-458

APPROXIMATE SURVEY/
COUNTY LINE

THE VINCENTE MICHELI SURVEY, A-29
ANGELINA COUNTY, TEXAS

VINCENTE MICHELI
SURVEY, A-29

APPROXIMATE SURVEY/
COUNTY LINE

LINE	BEARING	DISTANCE
L1	S 89°34'40" W	790.24'
L2	N 25°40'40" W	1081.10'
L3	N 04°52'09" W	9114.90'

STONEROLLER UNIT

TRACT	OWNER	ACREAGE
1	Black Stone Minerals Company, LP, et al.	664.752
2	Black Stone Minerals Company, LP, et al.	26.133
3	Black Stone Minerals Company, LP, et al.	4.480
4	Black Stone Minerals Company, LP, et al.	81.02
5	Black Stone Minerals Company, LP, et al.	4.99
6	Black Stone Minerals Company, LP, et al.	24.9397
7	Black Stone Minerals Company, LP, et al.	24.1809
8	Black Stone Minerals Company, LP, et al.	24.0419
9	DMV Interest, LLC	23.8682
10	Stephen Leggett, et al.	43.1
11	Eloise Brazil Richardson	34.008
TOTAL		955.5137

SURFACE HOLE LOCATION
STONEROLLER 1HB WELL
STATE PLANE COORDINATES—
TX-C-ZONE-NAD 27:
N: 685211 E: 3765445
GEOGRAPHIC-NAD 27:
LAT: 31.42714704 LONG: 94.67071343
GROUND ELEV: 229.6'
UNIT CALLS: 129' (SC) FEL AND 4463' (SC)
FSL OF THE STONEROLLER UNIT
SURVEY CALLS: 3806' (SC) FSEL AND 12194'
(SC) FSL OF THE VINCENTE MICHELI SVY,
A-29

PENETRATION POINT
STATE PLANE COORDINATES—
TX-C-ZONE-NAD 27:
N: 685205 E: 3764655
GEOGRAPHIC-NAD 27:
LAT: 31.42724157 LONG: 94.67324460
UNIT CALLS: 1977' (SC) FWL AND 4498' (SC)
FSL OF THE STONEROLLER UNIT
SURVEY CALLS: 4532' (SC) FSEL AND 13923'
(SC) FSL OF THE VINCENTE MICHELI SVY,
A-29

FIRST TAKE POINT
STATE PLANE COORDINATES—
TX-C-ZONE-NAD 27:
N: 686179 E: 3764186
GEOGRAPHIC-NAD 27:
LAT: 31.42998239 LONG: 94.67458573
UNIT CALLS: 1526' (SC) FWL AND 5495' (SC)
FSL OF THE STONEROLLER UNIT
SURVEY CALLS: 5550' (SC) FSEL AND 17217'
(SC) FSL OF THE VINCENTE MICHELI SVY,
A-29

LAST TAKE POINT/BOTTOM HOLE LOCATION
STATE PLANE COORDINATES—
TX-C-ZONE-NAD 27:
N: 695261 E: 3763413
GEOGRAPHIC-NAD 27:
LAT: 31.45502769 LONG: 94.67558273
UNIT CALLS: 1690' (SC) FEL AND 552' (SC)
FNL OF THE STONEROLLER UNIT
SURVEY CALLS: 4572' (SC) FEL AND 594'
(SC) FNL OF THE VINCENTE MICHELI SVY,
A-29

Surface Location is situated approximately 6.9 miles
Northeast of Lufkin, Texas.



Bearings and Coordinates are based on the State Plane
Coordinate System, NAD 1927, Texas Central Zone.

NOTE: This plat does not, in any way, represent a
"Boundary Survey," and does not comply with current
T.B.P.L.S. Minimum Standards of Practice for Boundary
Surveys. Acreages and title information shown herein
were furnished by others. The information contained
on this plat is intended for the sole use of CATURUS
ENERGY, LLC.



I CERTIFY THAT THIS PLAT IS AN ACCURATE
REPRESENTATION OF AN ACTUAL ON-THE-GROUND
SURVEY MADE UNDER MY DIRECT SUPERVISION.

Michael Casey Griffis 07/30/2026
MICHAEL CASEY GRIFFIS R.P.L.S. 6959 DATE

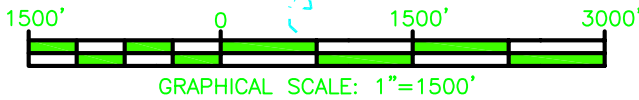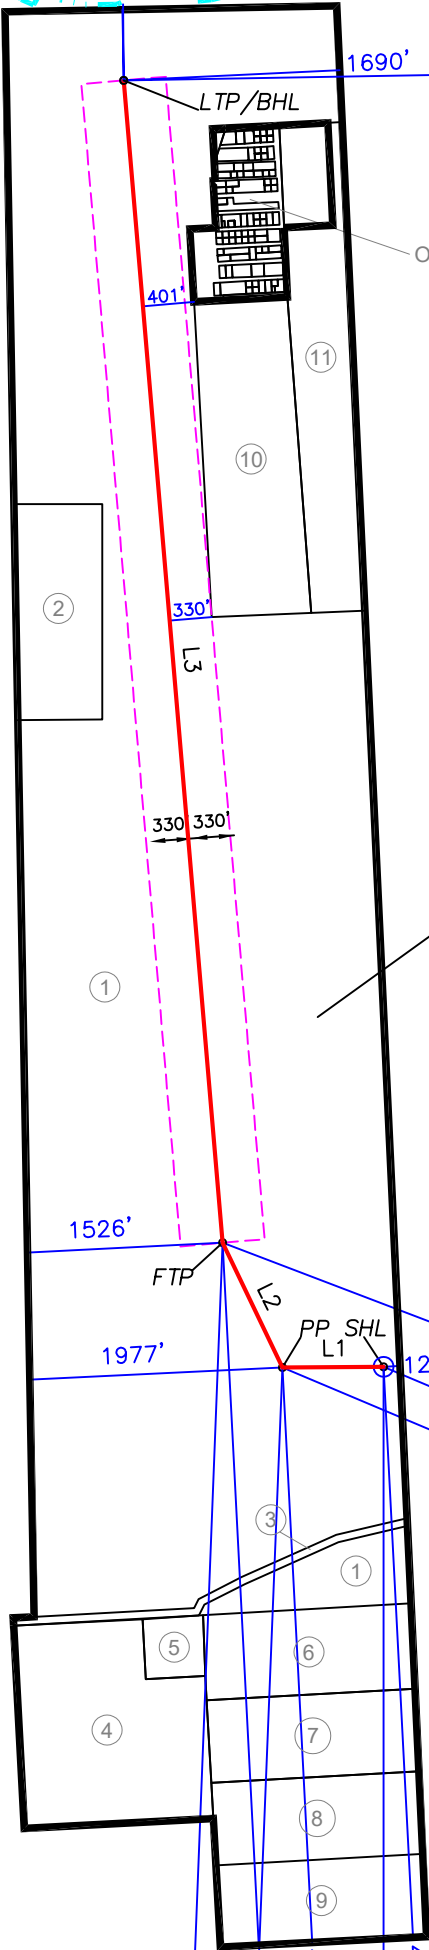

PLAT SHOWING:

STONEROLLER UNIT AND
STONEROLLER 1HB
WELL PERMIT
CATURUS ENERGY, LLC

Bowman

4901 E End Blvd South, Marshall, Tx 75672
www.bowman.com | 903.471.8391
TBPELS Firm No. 10120600
LA Firm No. 846

JOB NO: 382098	REVISION : 0
FW BY: JKD/DS	SCALE 1"= 1500'
DRAWN BY: CML	SHEET 1 OF 1
CHKD BY: MCG	DATE: 07/30/26